
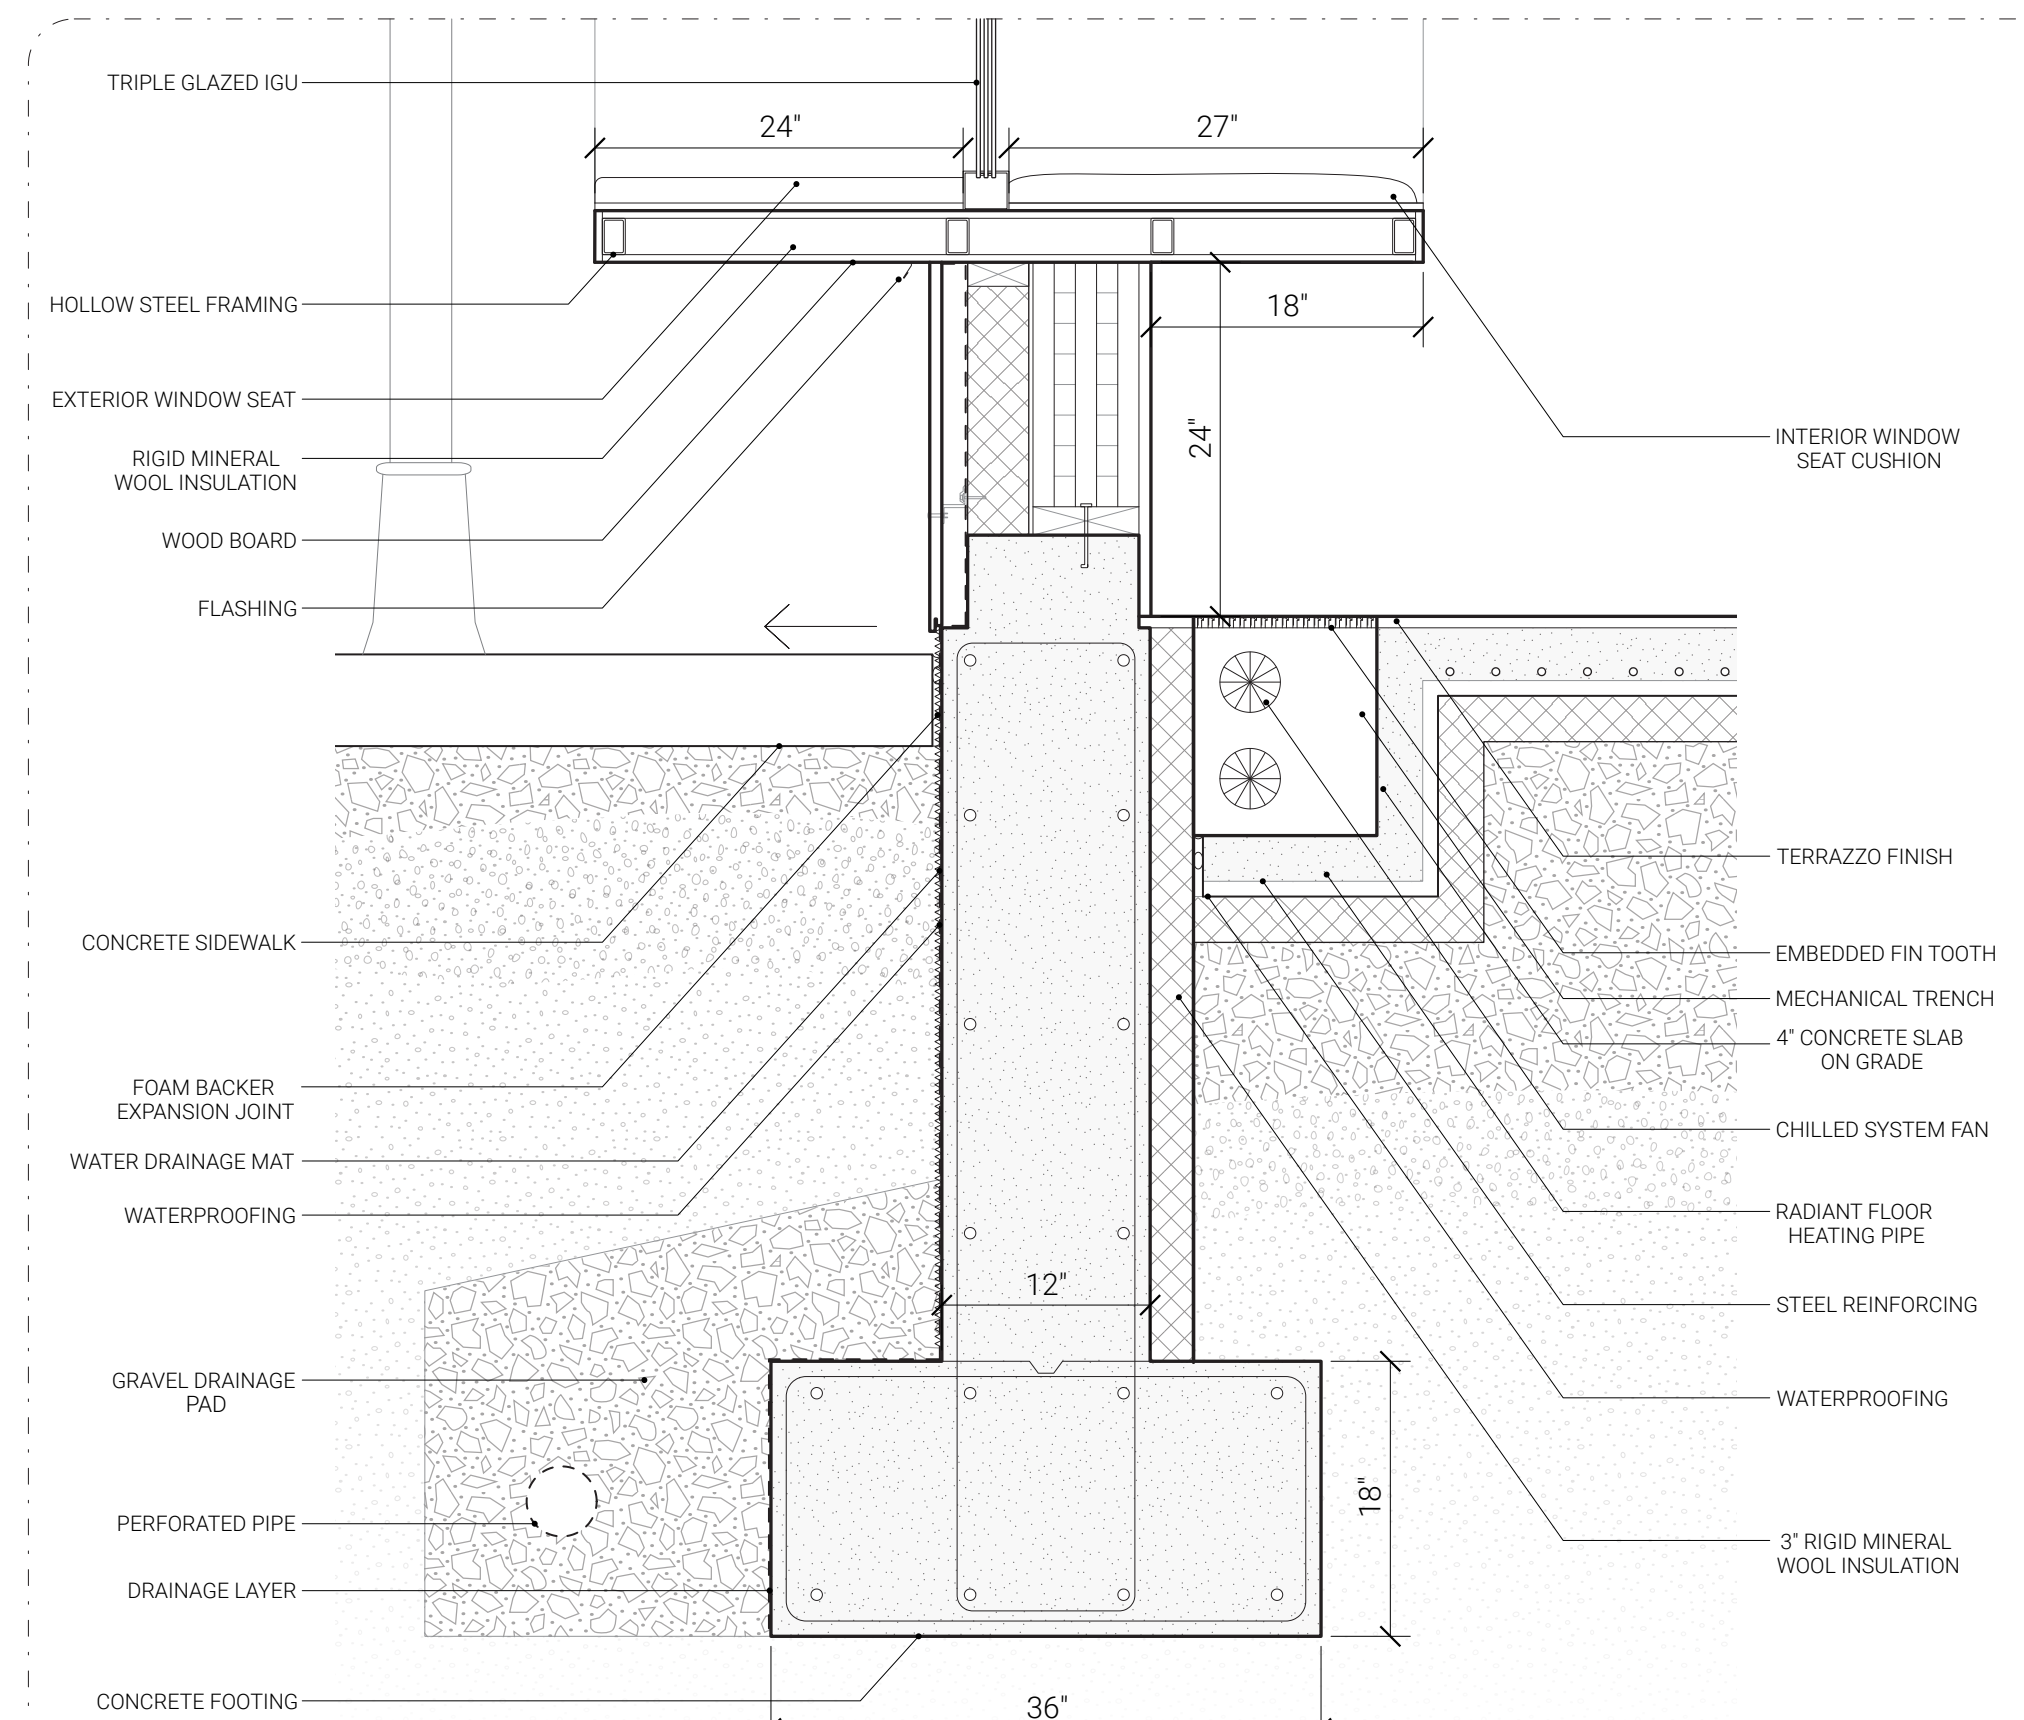
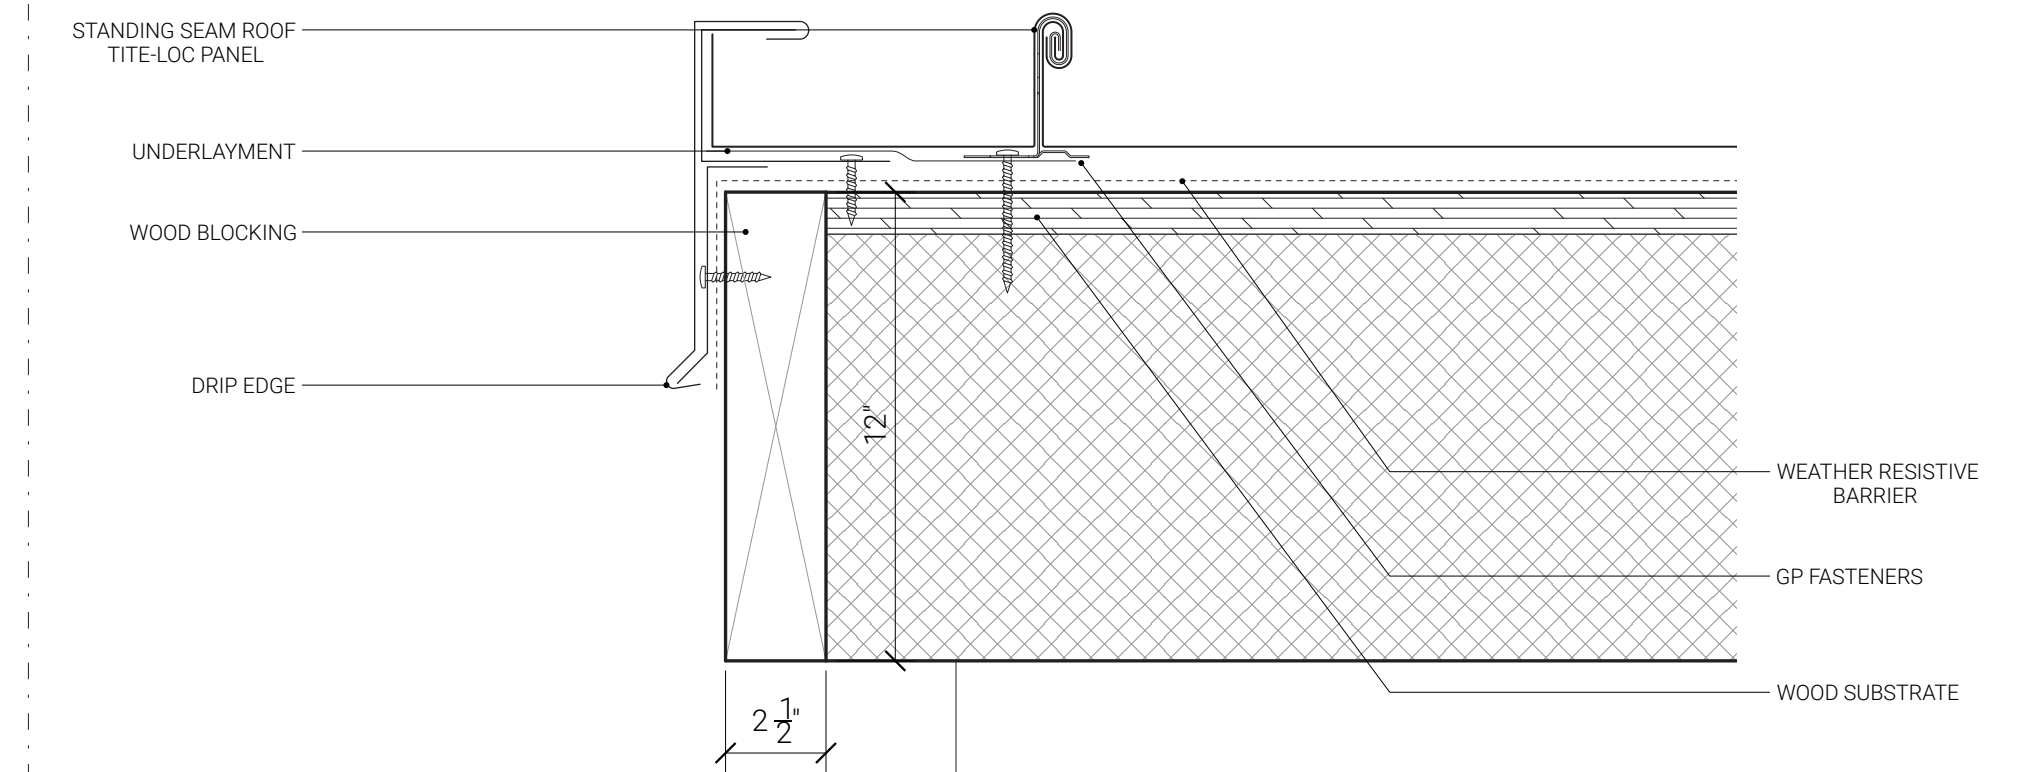


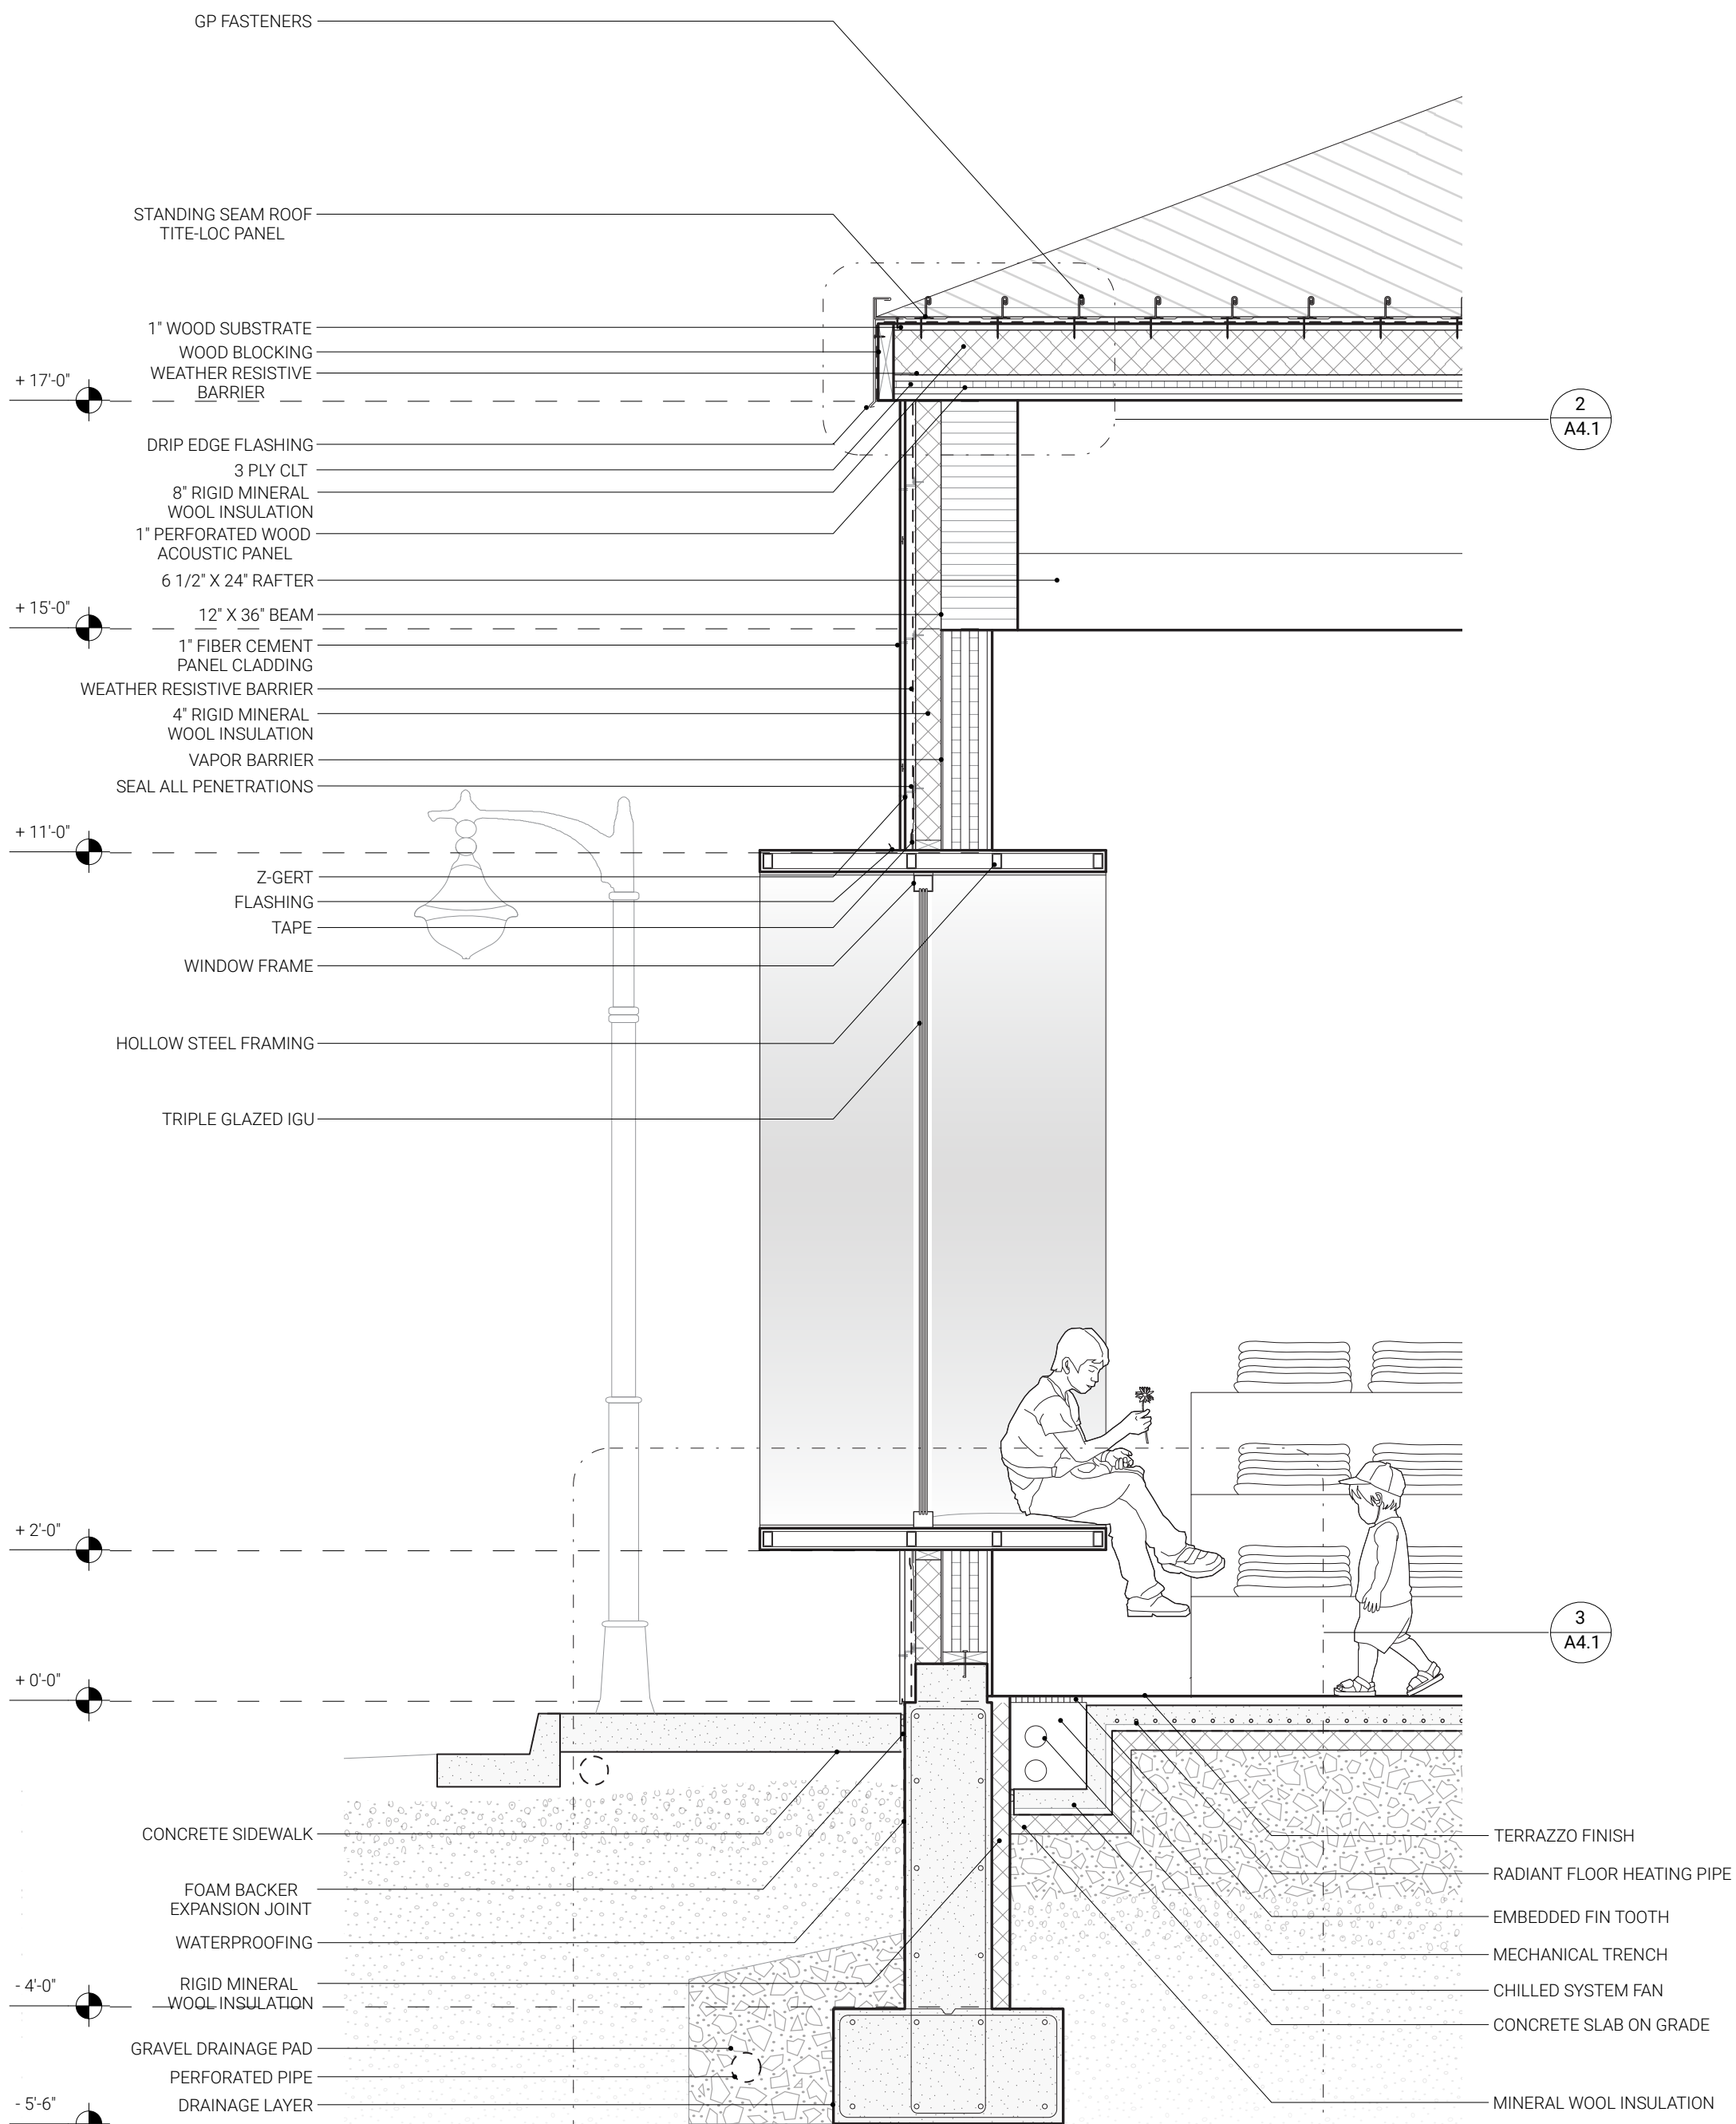

ARC
409

JUHI IDNANI
DIONESA KRUEZIU
KAY SMITH


PROJECT INFORMATION

PROJECT NAME: TOYWORKS
ADDRESS: 2176 Erie Blvd E
STATUS: DESIGN DEVELOPMENT

DRAWING

1

TITLE: WALL ASSEMBLY 1
DRAWN BY: KS & JI
DATE: 4/30/2026
SCALE: 1/2" = 1'-0"

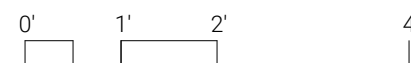

DRAWING (UP)

2

TITLE: WALL ASSEMBLY DETAIL 1
DRAWN BY: KS & JI
DATE: 4/30/2026
NOT TO SCALE




DRAWING (DOWN)

3

TITLE: WALL ASSEMBLY DETAIL 2
DRAWN BY: KS & JI
DATE: 4/30/2026
NOT TO SCALE

sheet no.
plan

A4.1

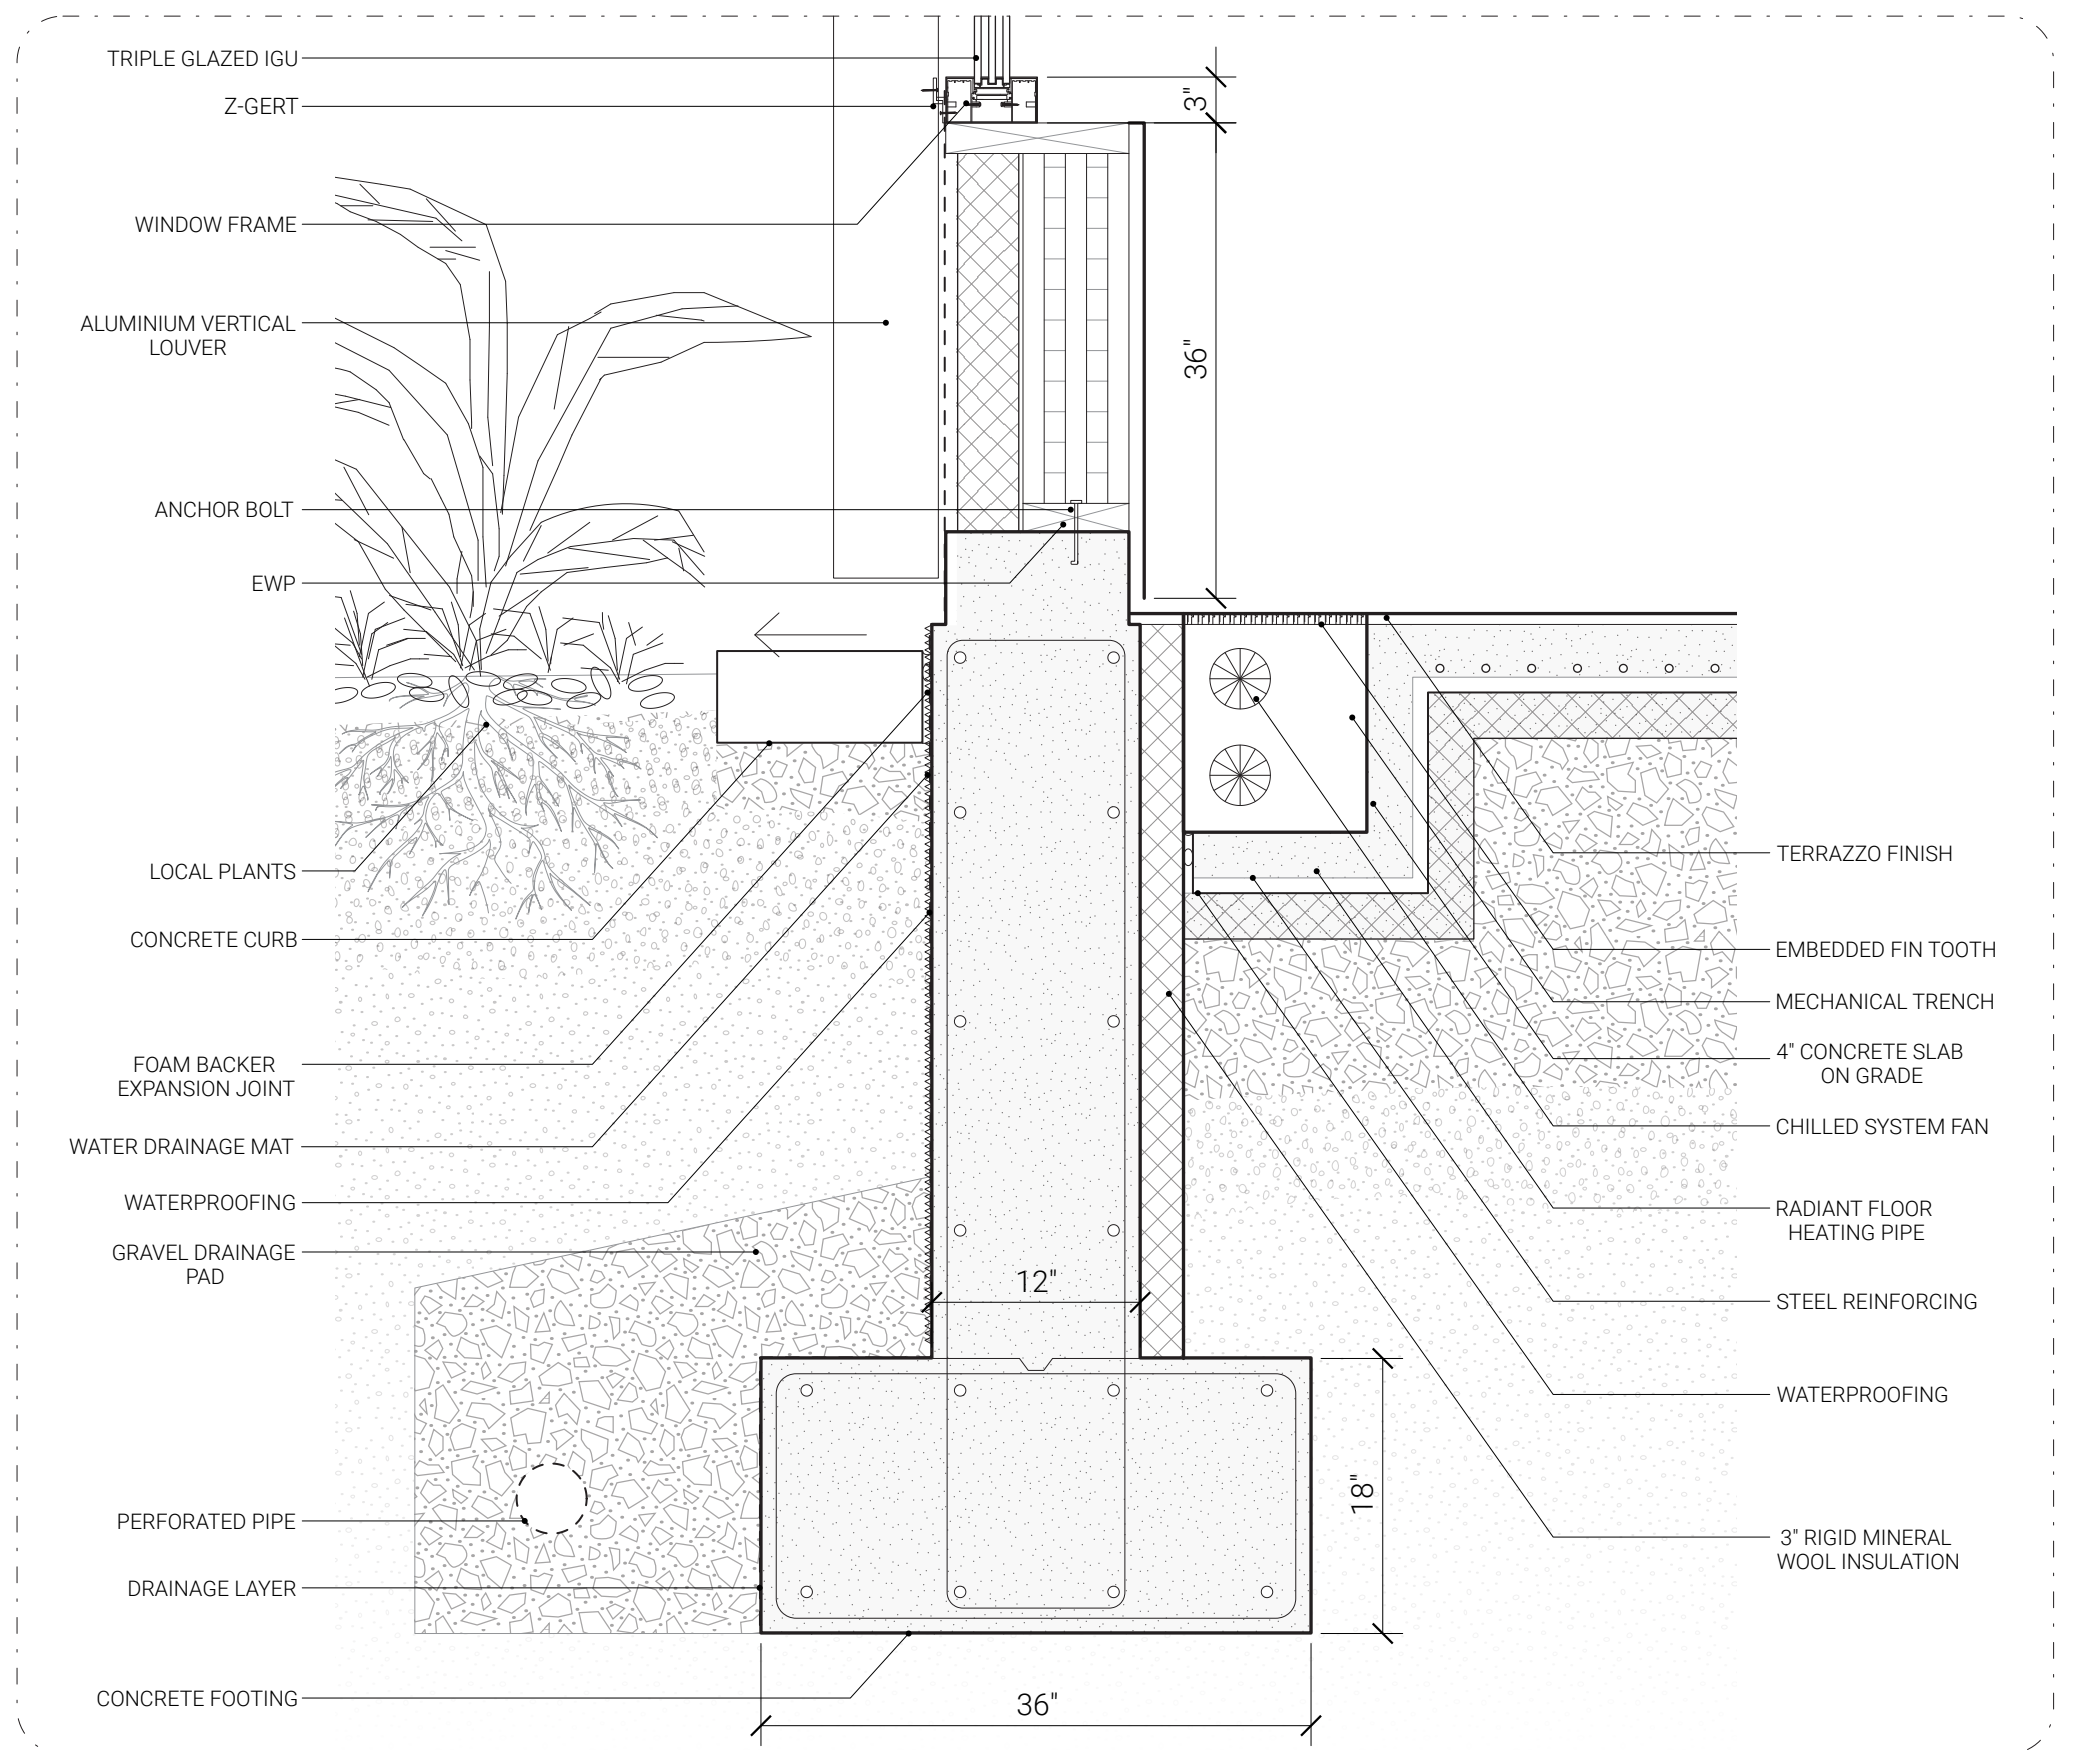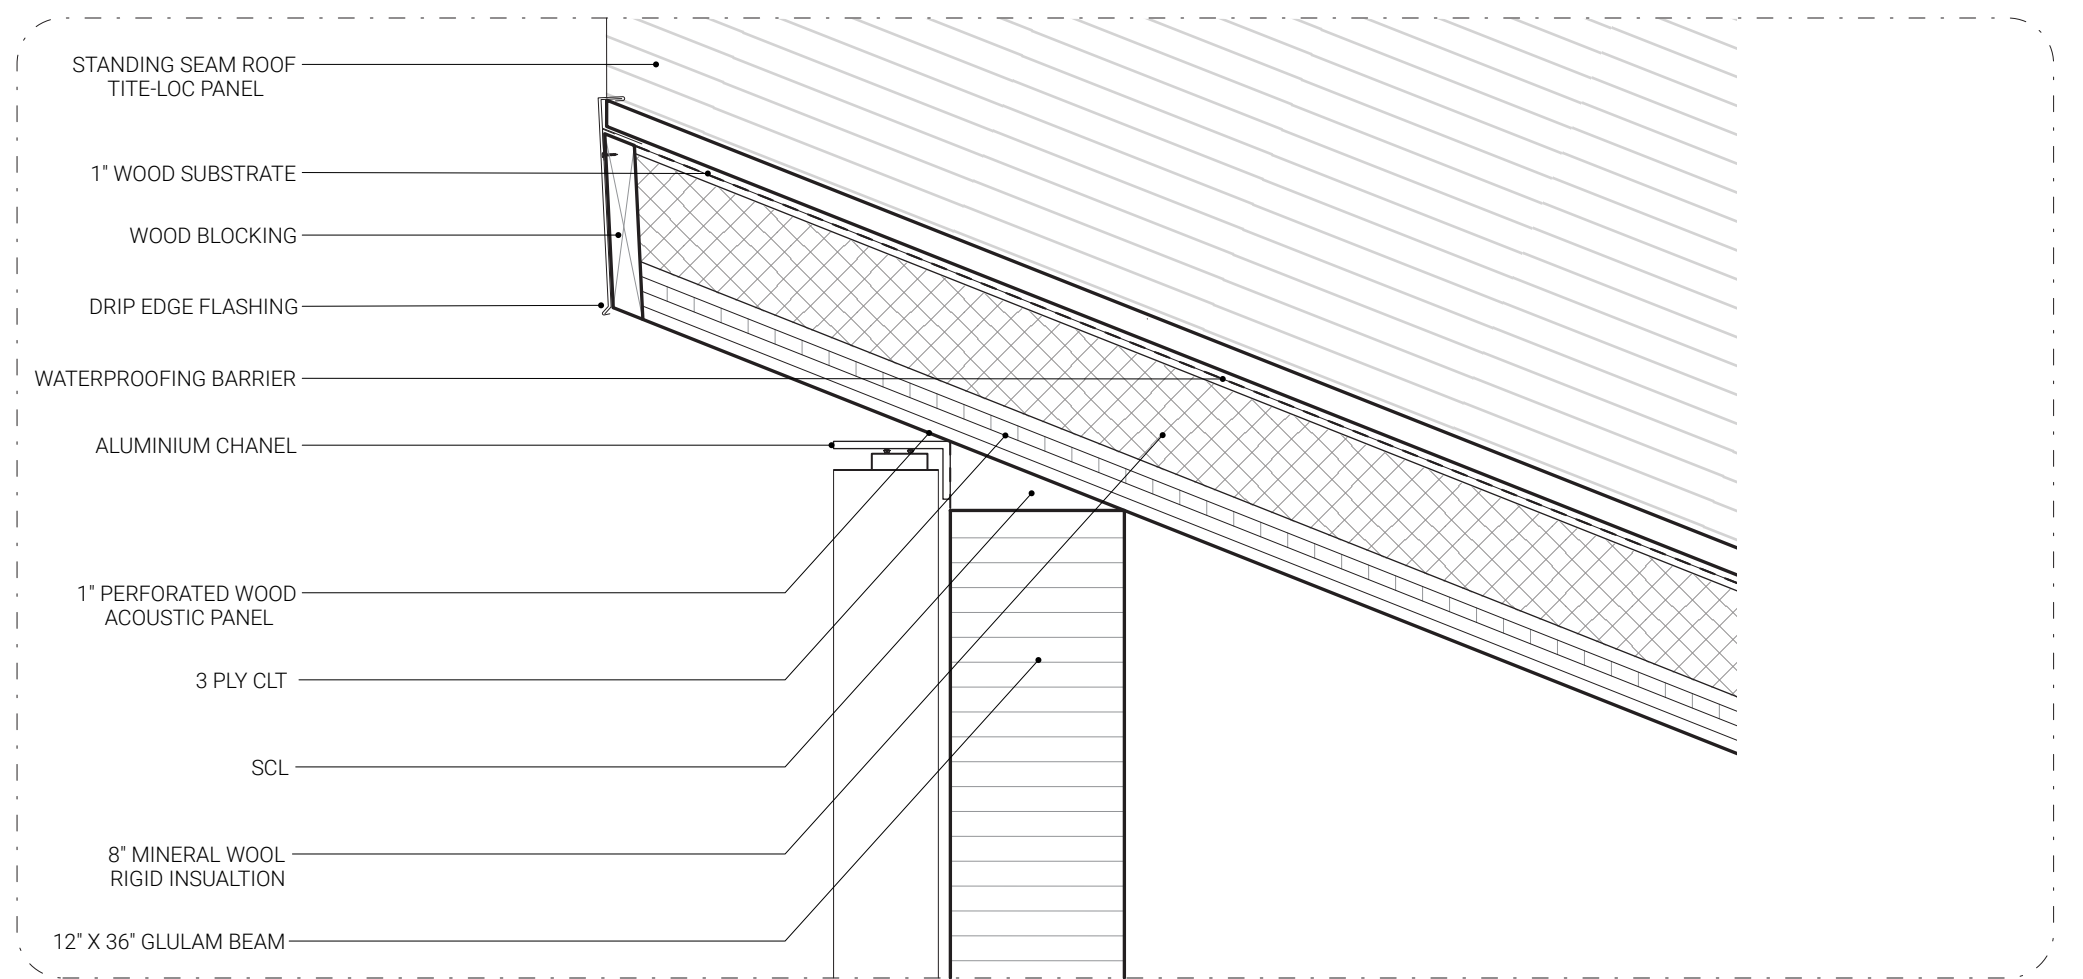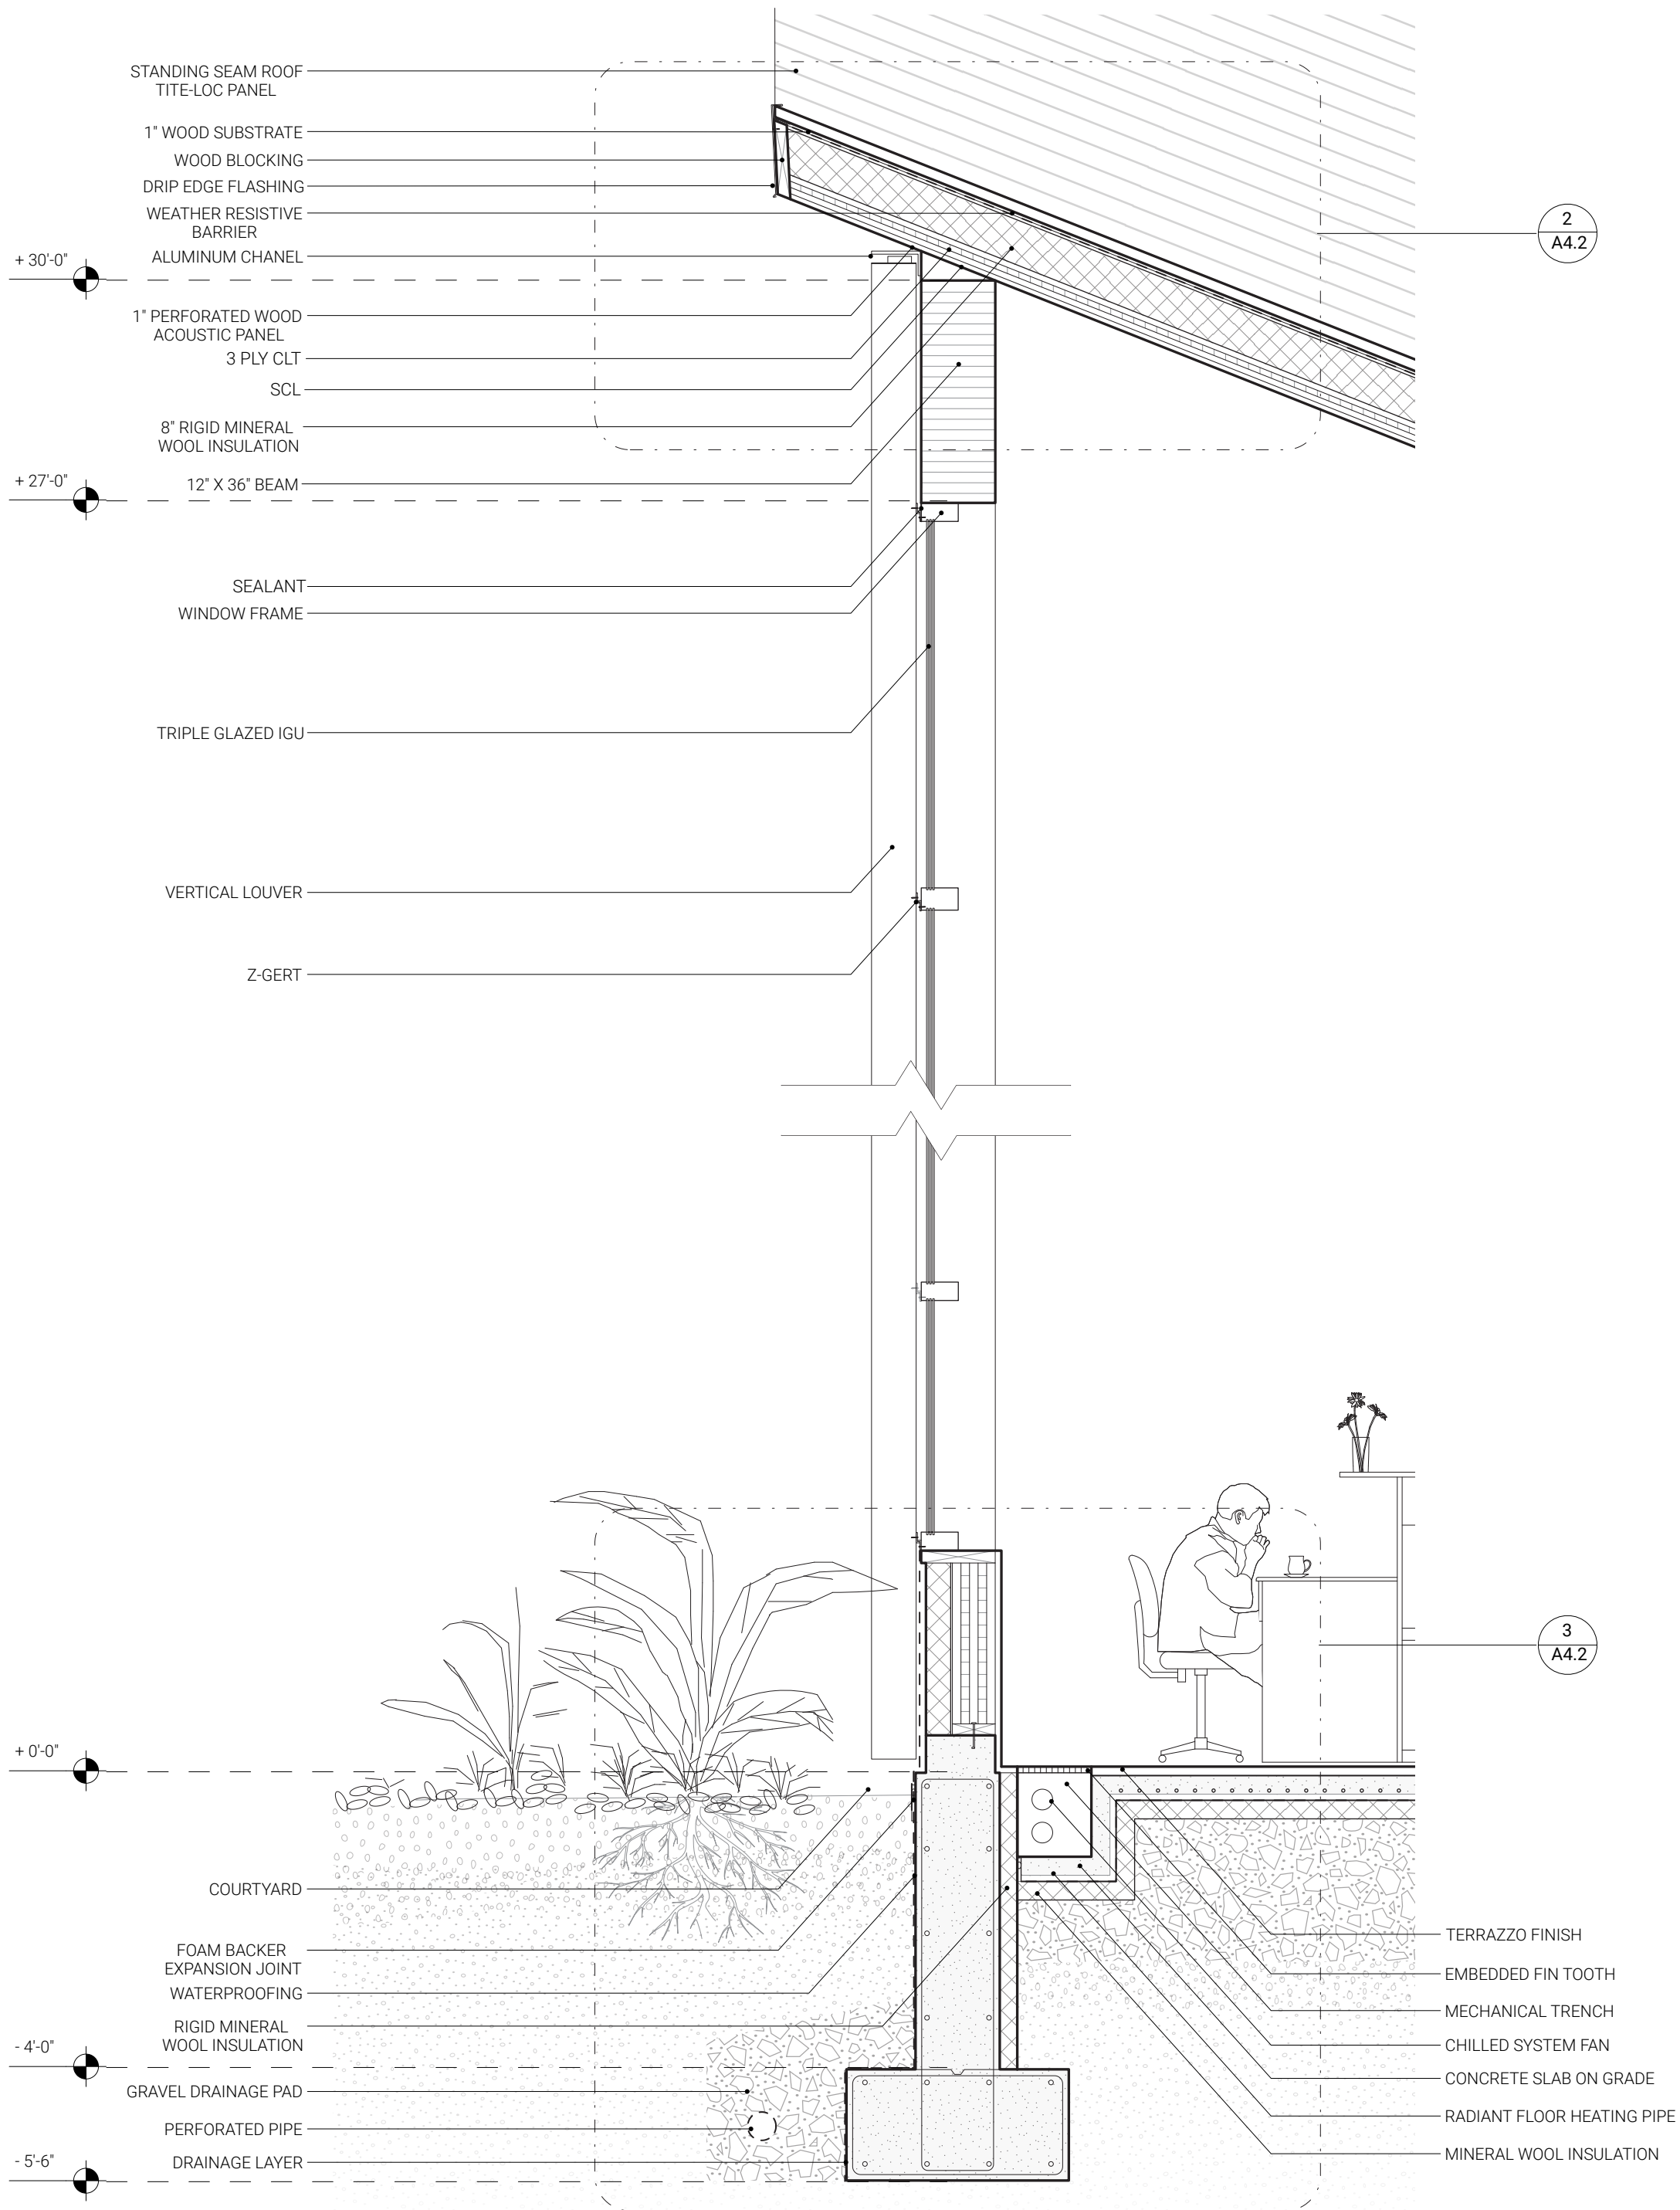

ARC
409

JUHI IDNANI
DIONESA KRUEZIU
KAY SMITH

PROJECT INFORMATION

PROJECT NAME: TOYWORKS
ADDRESS: 2176 Erie Blvd E
STATUS: DESIGN DEVELOPMENT

DRAWING

1

TITLE: WALL ASSEMBLY 2
DRAWN BY: KS & JI
DATE: 4/30/2026
SCALE: 1/2" = 1'-0"

0' 1' 2' 4'

DRAWING (UP)

2

TITLE: WALL ASSEMBLY DETAIL 3
DRAWN BY: KS & JI
DATE: 4/30/2026
NOT TO SCALE




DRAWING (DOWN)

3

TITLE: WALL ASSEMBLY DETAIL 4
DRAWN BY: KS & JI
DATE: 4/30/2026
NOT TO SCALE

sheet no.
plan

A4.2

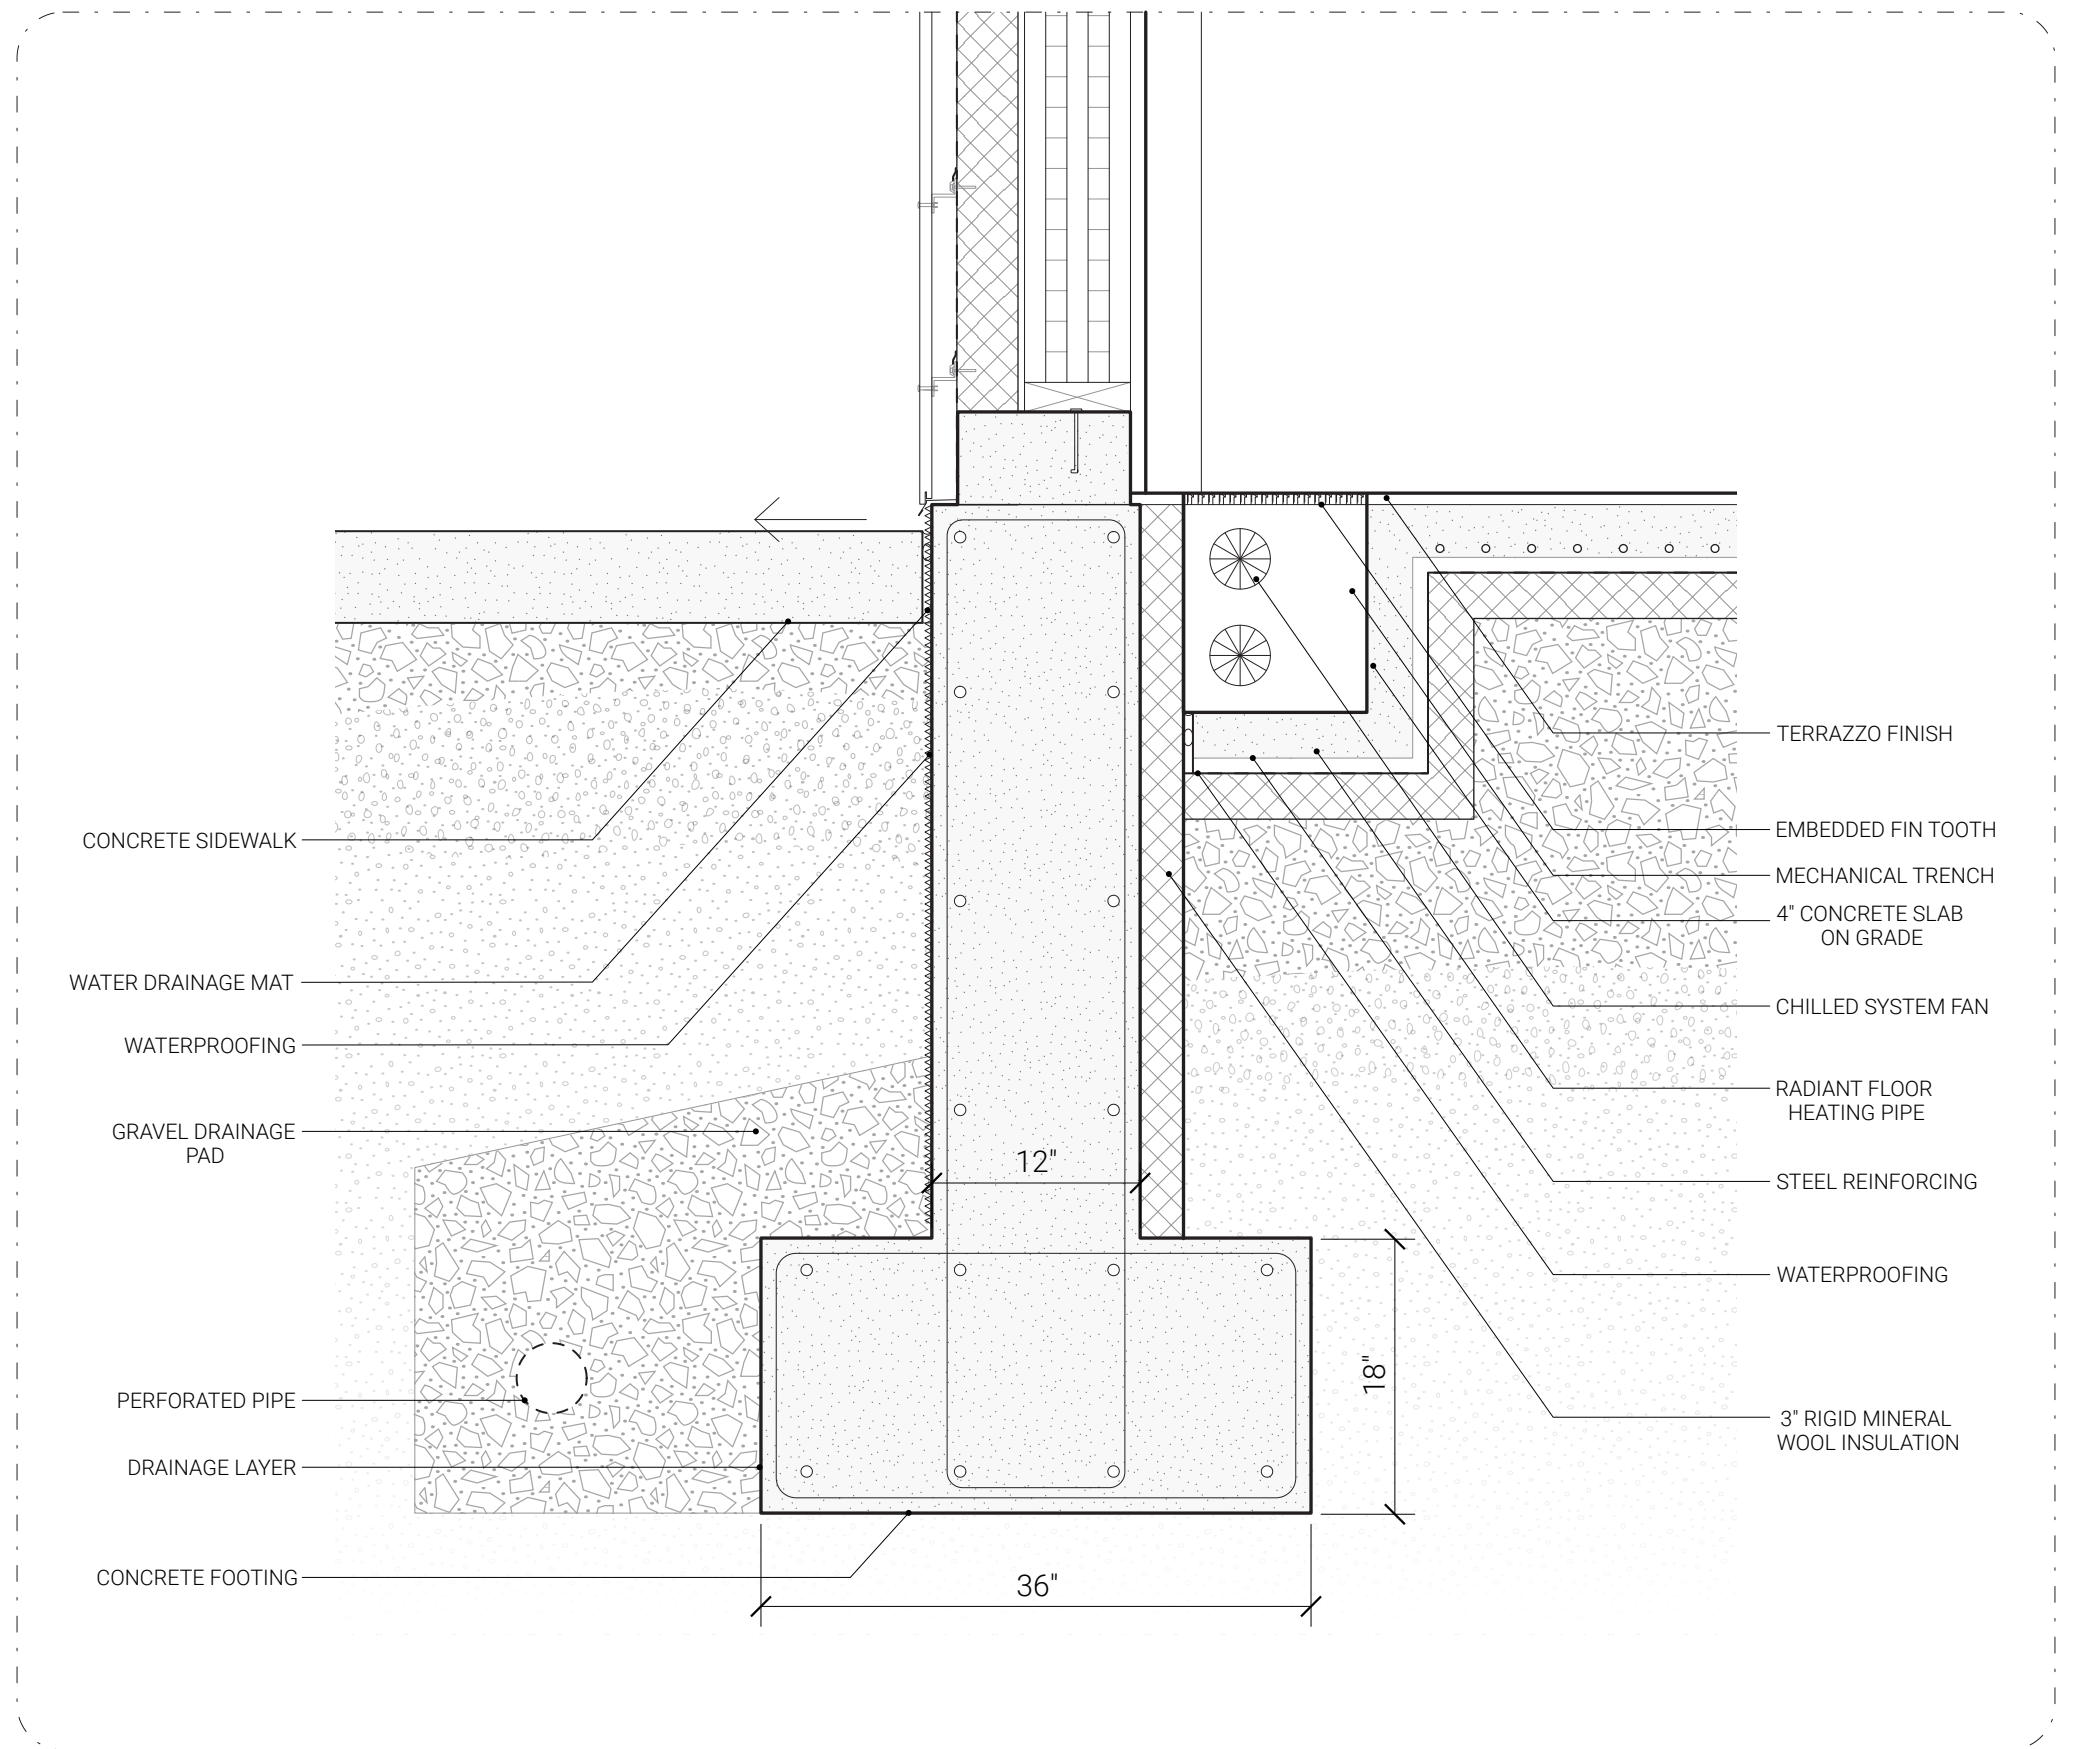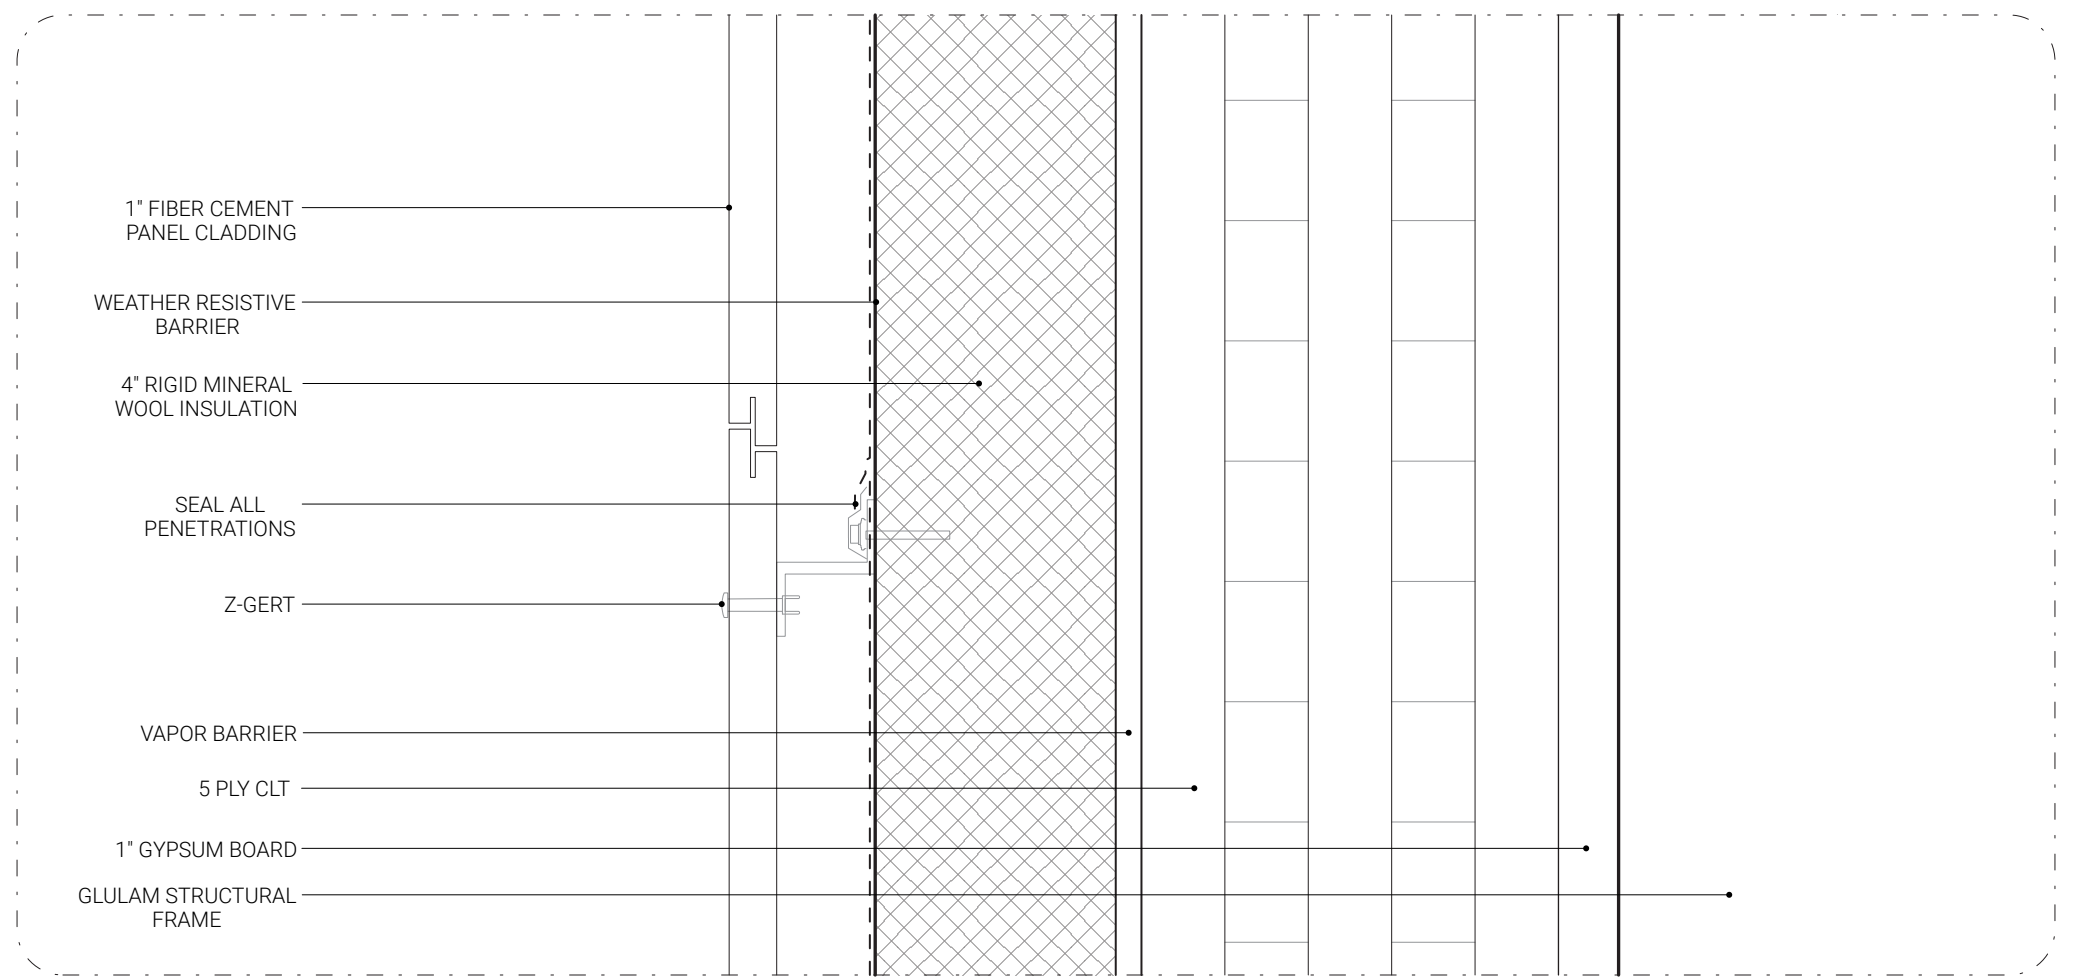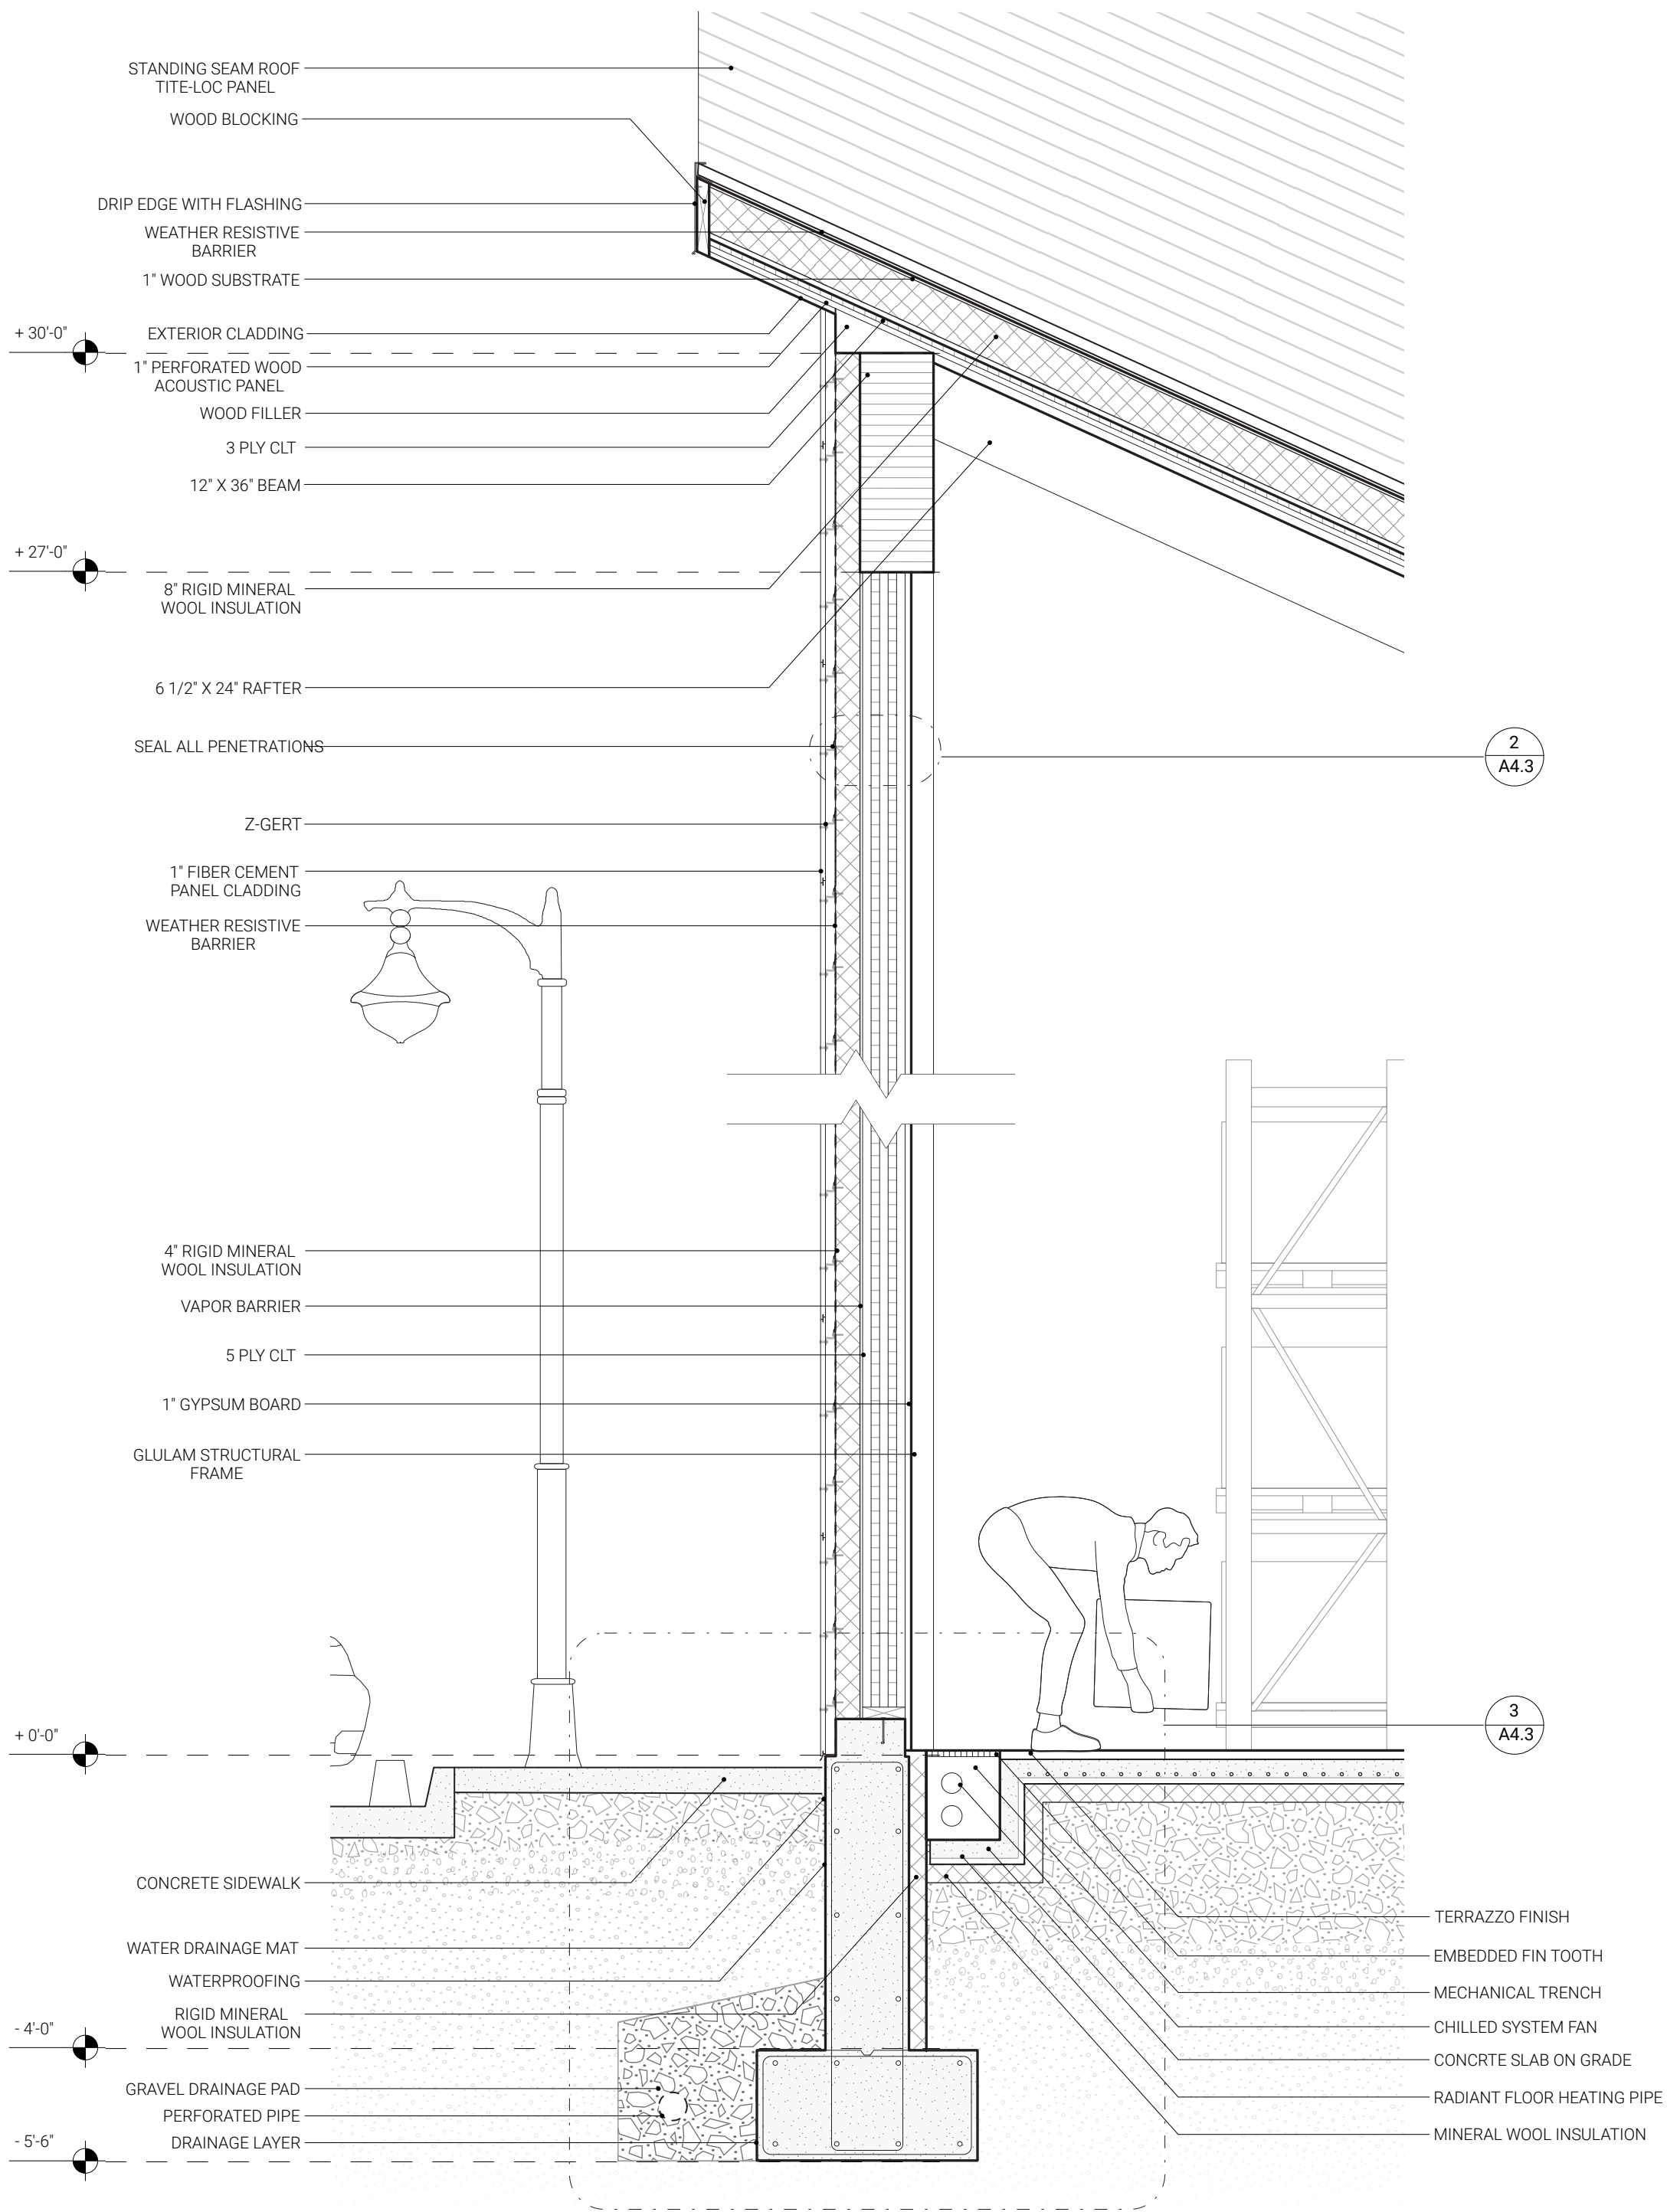

ARC
409

JUHI IDNANI
DIONESA KRUEZIU
KAY SMITH


PROJECT INFORMATION

PROJECT NAME: TOYWORKS
ADDRESS: 2176 Erie Blvd E
STATUS: DESIGN DEVELOPMENT

DRAWING

1

TITLE: WALL ASSEMBLY 3
DRAWN BY: KS & JI
DATE: 4/30/2026
SCALE: 1/2" = 1'-0"

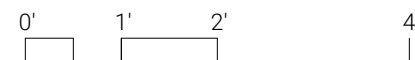

DRAWING (UP)

2

TITLE: WALL ASSEMBLY DETAIL 5
DRAWN BY: KS & JI
DATE: 4/30/2026
NOT TO SCALE

DRAWING (DOWN)

3

TITLE: WALL ASSEMBLY DETAIL 6
DRAWN BY: KS & JI
DATE: 4/30/2026
NOT TO SCALE

sheet no.
plan

A4.3