




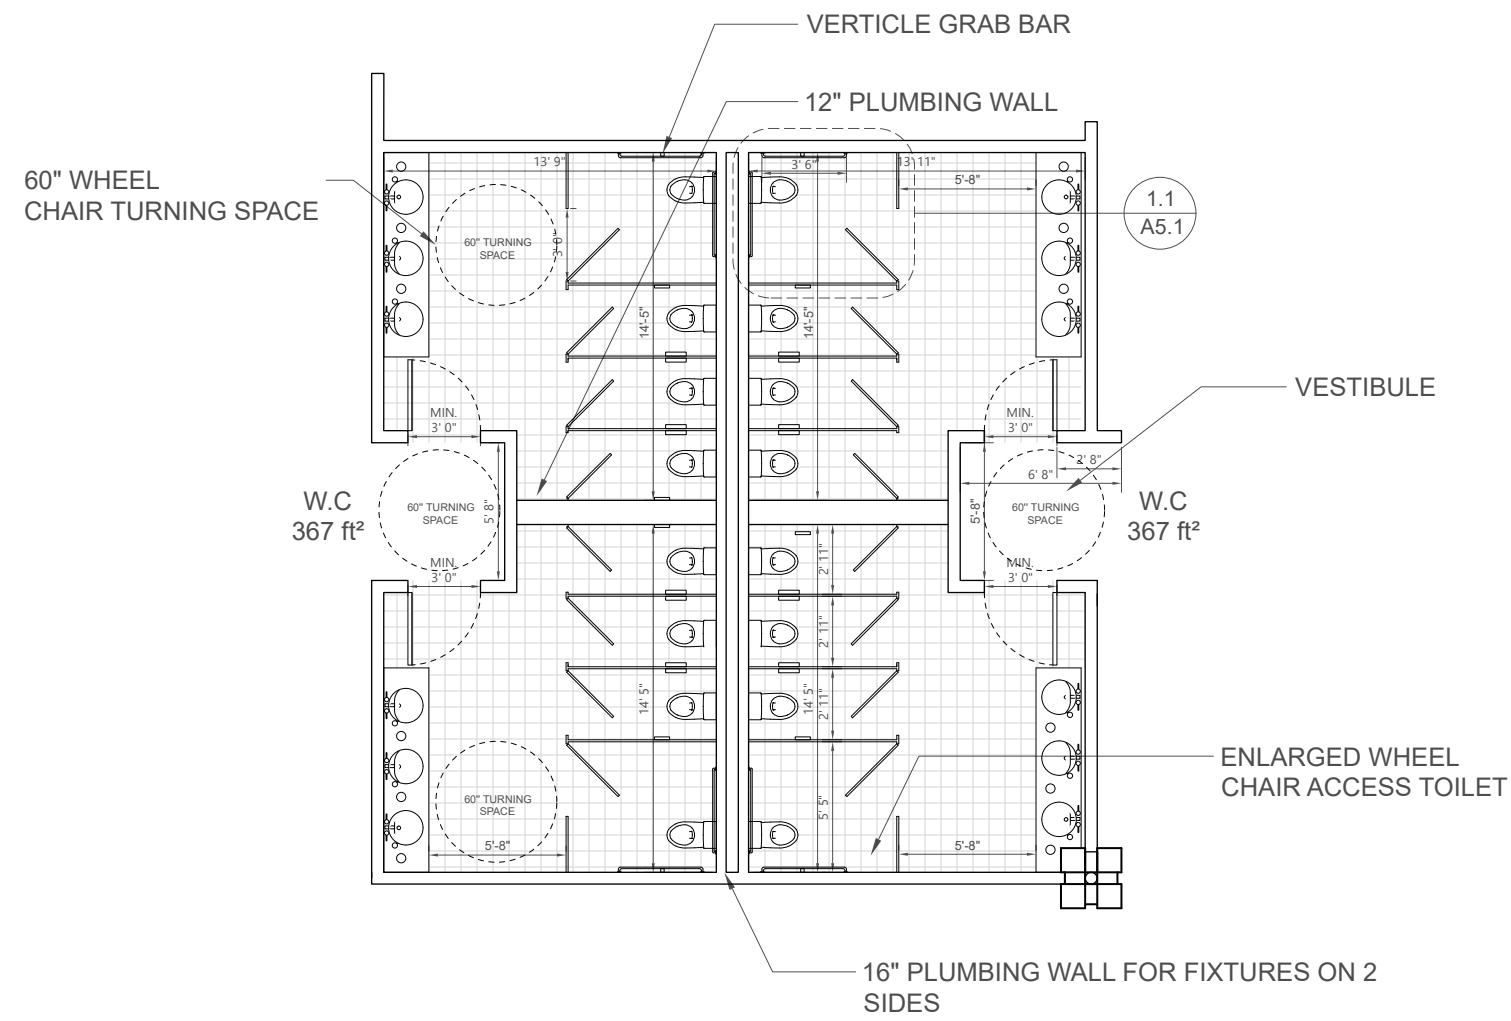


ADA BATHROOM
SCALE: 1/8" = 1'-0"

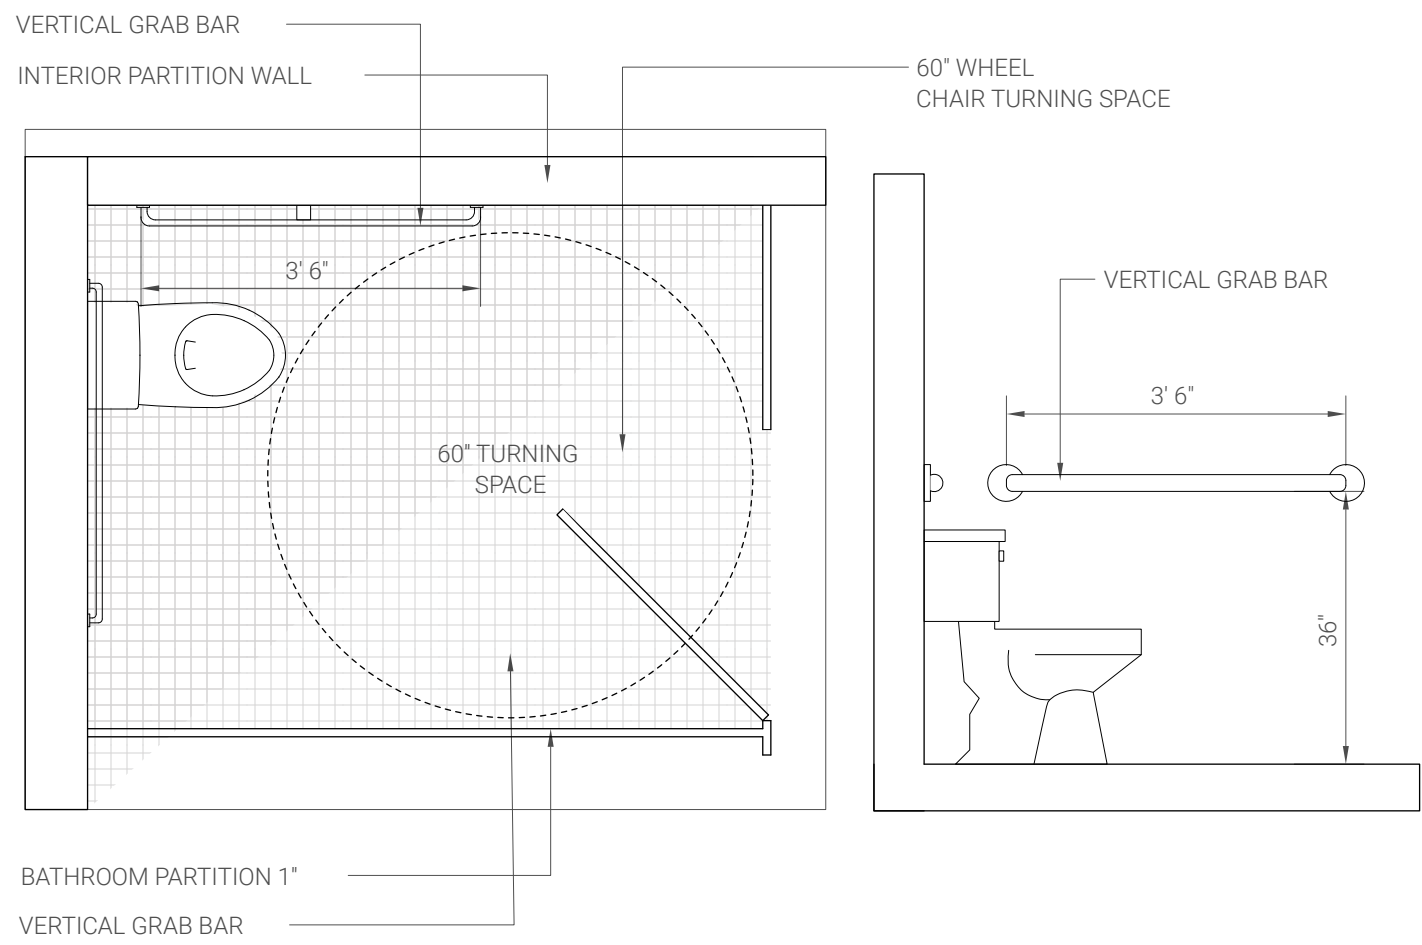

ADA BATHROOM DETAIL
SCALE: 1/2" = 1'-0"

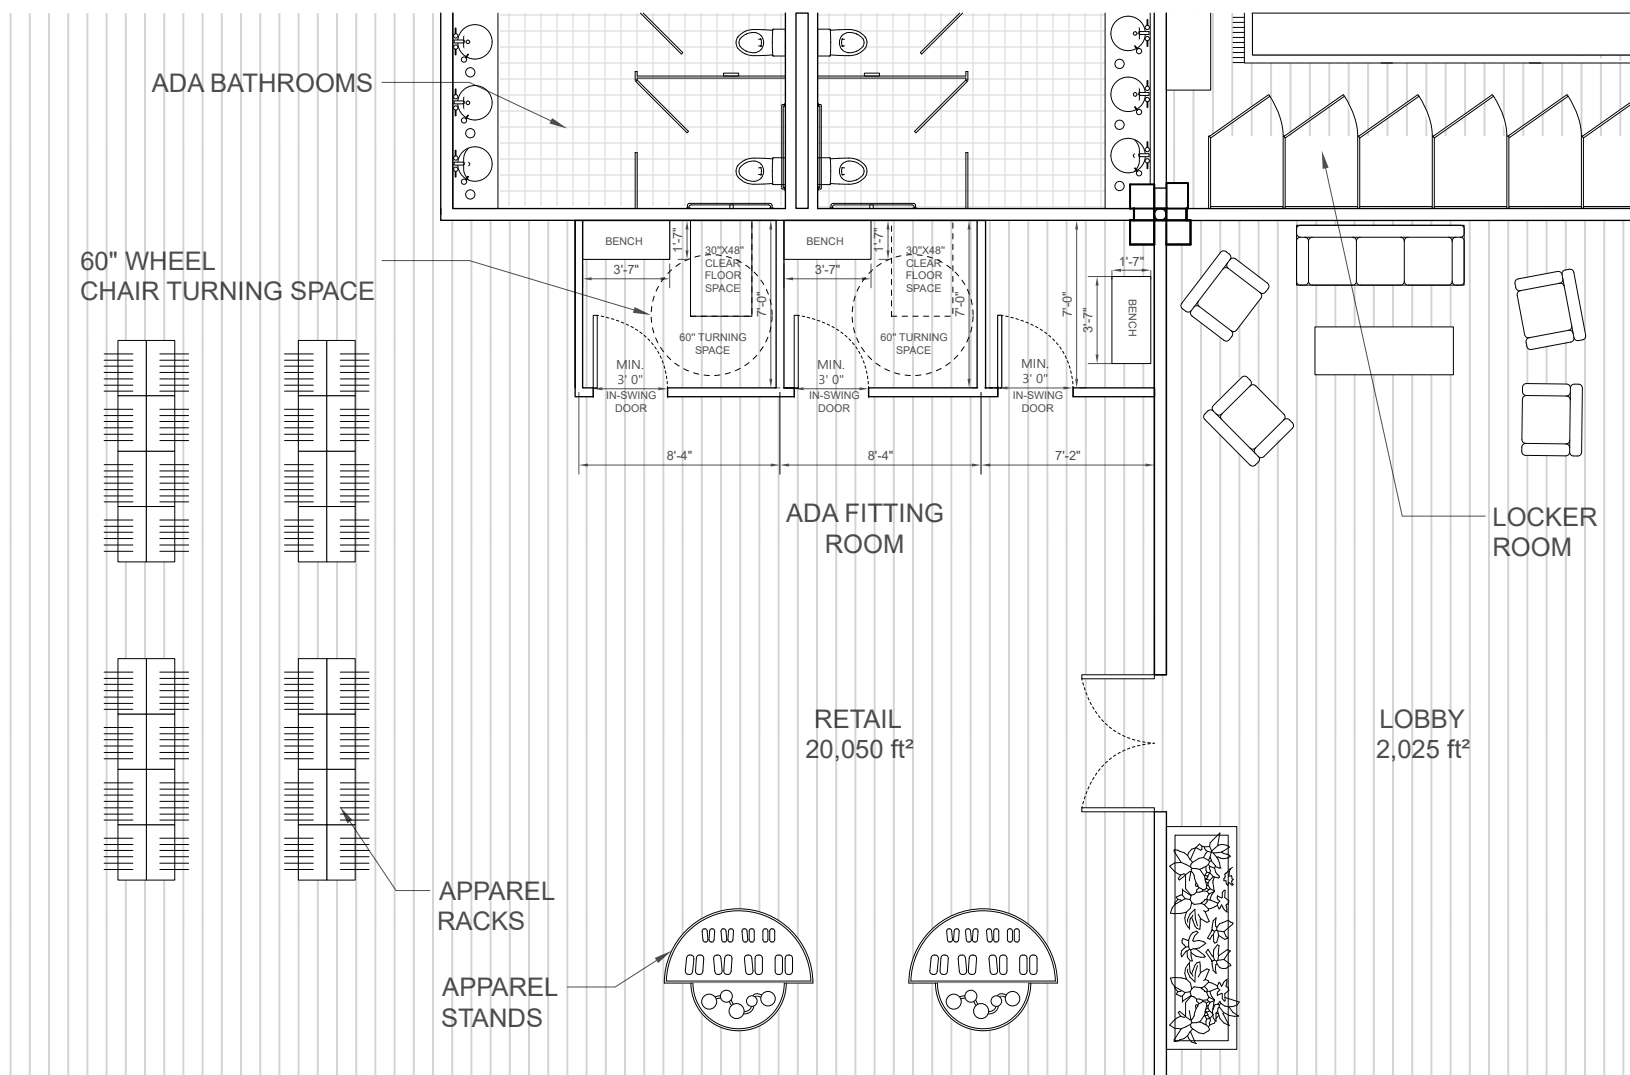

ADA FITTING ROOMS
SCALE: 1/8" = 1'-0"

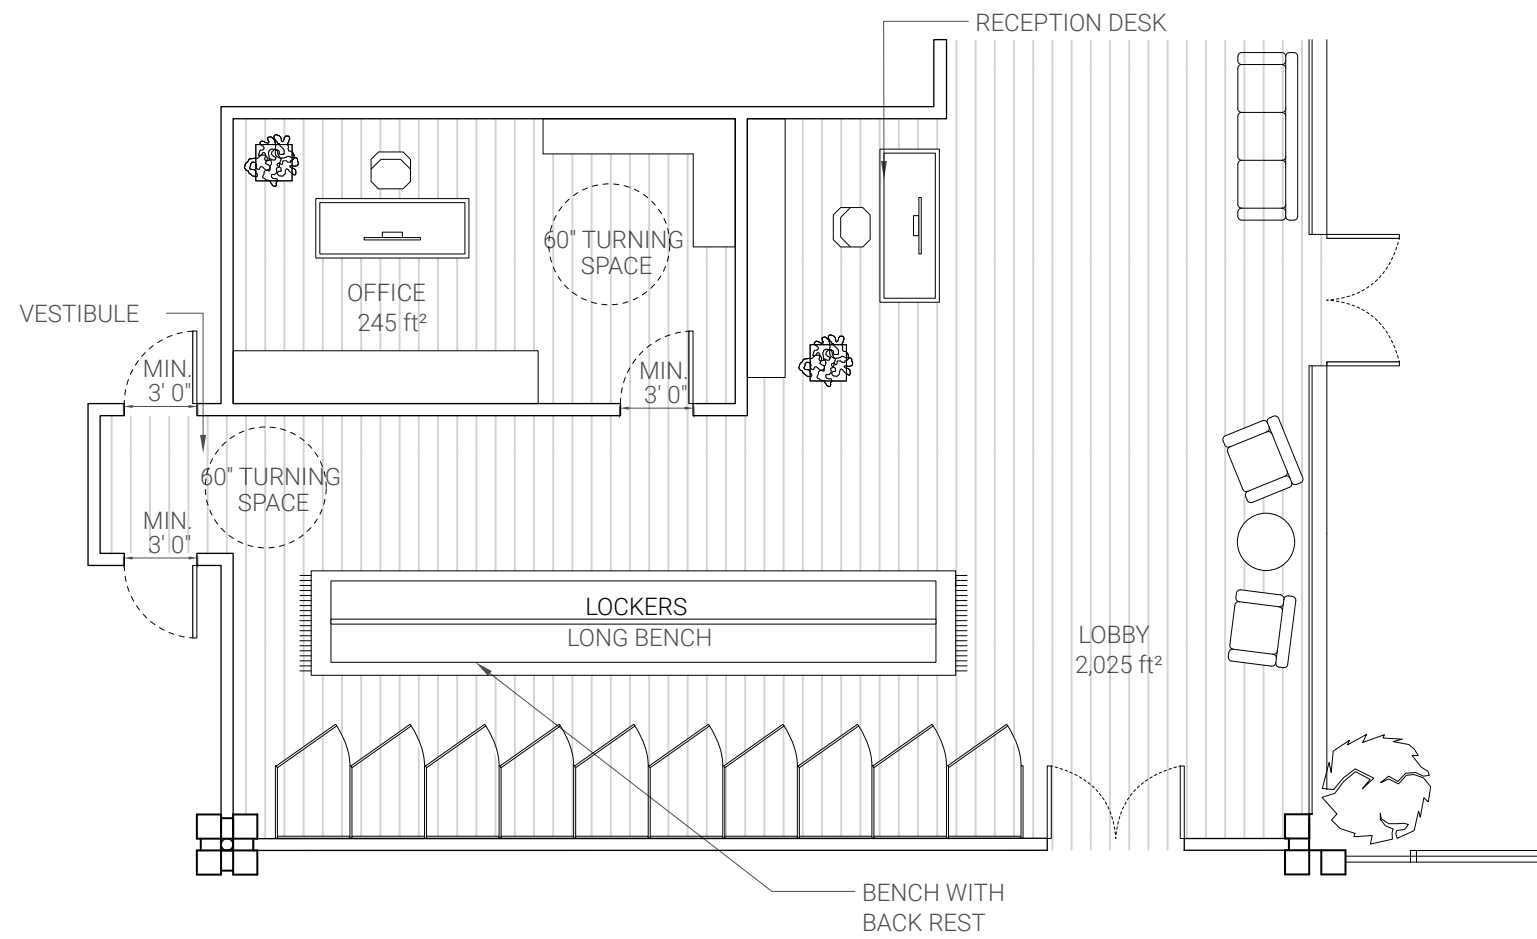

LOCKER ROOMS
SCALE: 1/8" = 1'-0"

ARC
409

DIONESA KRUEZIU
JUHI IDNANI
KAY SMITH

TRUE NORTH



NOTES

ADA BATHROOM
1/8" = 1'-0"

ADA BATHROOM DETAIL
1/2" = 1'-0"

ADA FITTING ROOMS
1/8" = 1'-0"

LOCKER ROOMS
1/8" = 1'-0"


PROJECT INFORMATION

PROJECT NAME: TOYWORKS
ADDRESS: 2176 ERIE BLVD E
STATUS: DESIGN DEVELOPMENT

DRAWING

1

TITLE: DETAILS
DRAWN BY: DK & KS
DATE: 4/30/2026
SCALE: 1/8" = 1'-0"

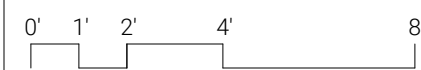

sheet no.
plan

A5.1