

PROJECT INFORMATION

PROJECT TITLE: **TOYWORKS**
COURSE: ARC 409 Integrative Design Studio
SECTION: Timber Big-Box, Studio Erar
TERM: Spring 2026

PROJECT DESCRIPTION

Toyworks is an experiential space for children in Syracuse that reimagines the big-box toy store as a place for play, learning, and community. Built with sustainable mass timber, the retail edge faces Erie Boulevard, while indoor play areas, exhibits, an outdoor playground and an educational daycare address the residential side. The project responds to the neighborhood's lack of safe indoor play spaces, creating a colorful environment that fosters creativity, discovery, and joy.


PROJECT TEAM

Architecture: Juhi Idnani, Dionesa Krueziu, Kay Smith
Structural: Sinead C Mac Namara, Bonghwan Kim
Facade: Stephen Weinbry

SITE INFORMATION AND VICINITY MAP

Address: 2176 Erie Boulevard E, Syracuse NY

SYRACUSE, NY

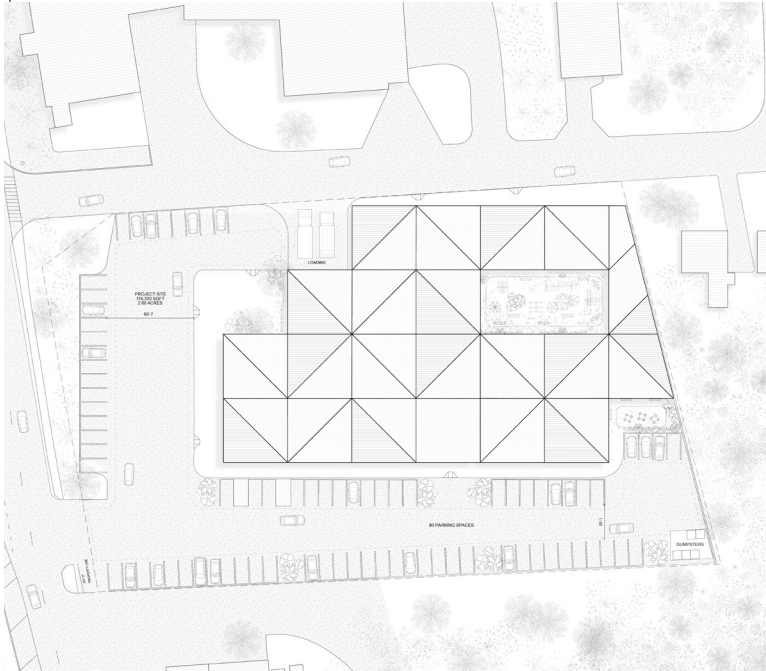

SHEET INDEX

G 1.0	GENERAL INFORMATION
A 1.1	EGRESS PLAN
A 1.2	GROUND FLOOR PLAN
A 1.3	SITE PLAN
A 2.1	NORTH AND WEST ELEVATIONS
A 2.2	SOUTH AND EAST ELEVATIONS
A 2.3	ELEVATION DETAIL
A 3.1	SECTIONS
A 4.1	WALL SECTION 1
A 4.2	WALL SECTION 2
A 4.3	WALL SECTION 3
A 5.1	DETAIL PLAN
S 1.1	FOUNDATION PLAN
S 1.2	STRUCTURAL FLOOR PLAN
S 3.1	STRUCTURAL SECTION
S 4.1	STRUCTURAL AXON
S 4.2	BAY AXON
S 4.3	CONNECTION DETAILS
M 1.1	HVAC PLAN
M 1.2	PLUMBING PLAN

APPLICABLE CODES

- Building Code of New York State 2025
- Energy Conservation Construction Code of NY State 2025
- 2025 Fire Code of NY State
- 2025 Plumbing Code of NY State

EGRESS CALCULATIONS

OCCUPANCY LOAD FACTORS

Mercantile (M)	30 gross
Storage, Stock, Shipping (S)	300 gross
Business Areas (B)	150 gross
Day Care (E)	35 gross

Mercantile : 20,050 SQFT / 30 = 668 OL

Day Care : 8,200 SQFT / 35 = 234 OL

Storage : 4,050 SQFT / 300 = 13 OL

Business Areas : 9,750 / 150 = 65 OL

Total = 980 OL

SPACES WITH ONE EXIT (TABLE 1006.2.1)
EXIT ACCESS TRAVEL DISTANCE MAX (1017.2)

OCCUPANCY	MAX OCCUPANT LOAD OF SPACE PER ENTRY (BCNYS 2025 1006.2.1)	MAX COMMON PATH OF EGRESS WITH AUTOMATIC SPRINKLER SYSTEM (FEET) (BCNYS 2025 1006.2.1)	EXIT ACCESS TRAVEL DISTANCE MAX (FEET) (BCNYS 2025 1017.2)
Mercantile (M)	49	75	250
Day Care (E)	49	75	250
Storage (S)	49	100	250
Business Areas (B)	49	100	300

- If you have more than max load, you need at least two exit doors.
- The minimum distance between two exits need to be 1/3 diagonal of the occupied room.
- Max Load between 1-500 requires 2 exists, 501-1000 requires 3 exits, and 1001 and up requires 4 exits.

KEY SYMBOLS

		SECTION
		INTERIOR ELEVATION
		ELEVATION MARK
		DETAIL CALLOUT



TITLE: SECTION PERSPECTIVE
DRAWN BY: DK
DATE: 4/30/2026
SCALE: 1/4" = 1'-0"

ARC
409

DIONESA KRUEZIU
JUHI IDNANI
KAY SMITH

sheet no.
plan

G1.0